

Image d'ambiance générée par IA à partir de la maquette 3D — non contractuelle

semac
SOCIÉTÉ D'ÉCONOMIE MIXTE
D'AMÉNAGEMENT ET DE CONSTRUCTION

Étude de faisabilité · capacité


Foyer de Jeunes Travailleurs

Mille Roches, Saint-André


ind 1 — scénario retenu · document de travail
OCTOBRE 2026

Adresse	573 chemin Mille Roches, 97440 Saint-André
Cadastre	BH 513 pour partie — partie est, ≈ 2 965 m²
Programme	FJT 60 logements LLTS · communs · pôle administratif MLE · micro-crèche 12 places — exploitant MLE
Zone PLU	**Ue** — équipements (PLU approuvé le 02/07/2025) · hébergement interdit : évolution du PLU requise
PPRN	B3 inondation · B2u en limite est
Dossier	MGA-26-04


Mathias Giraud Architecture mgA.

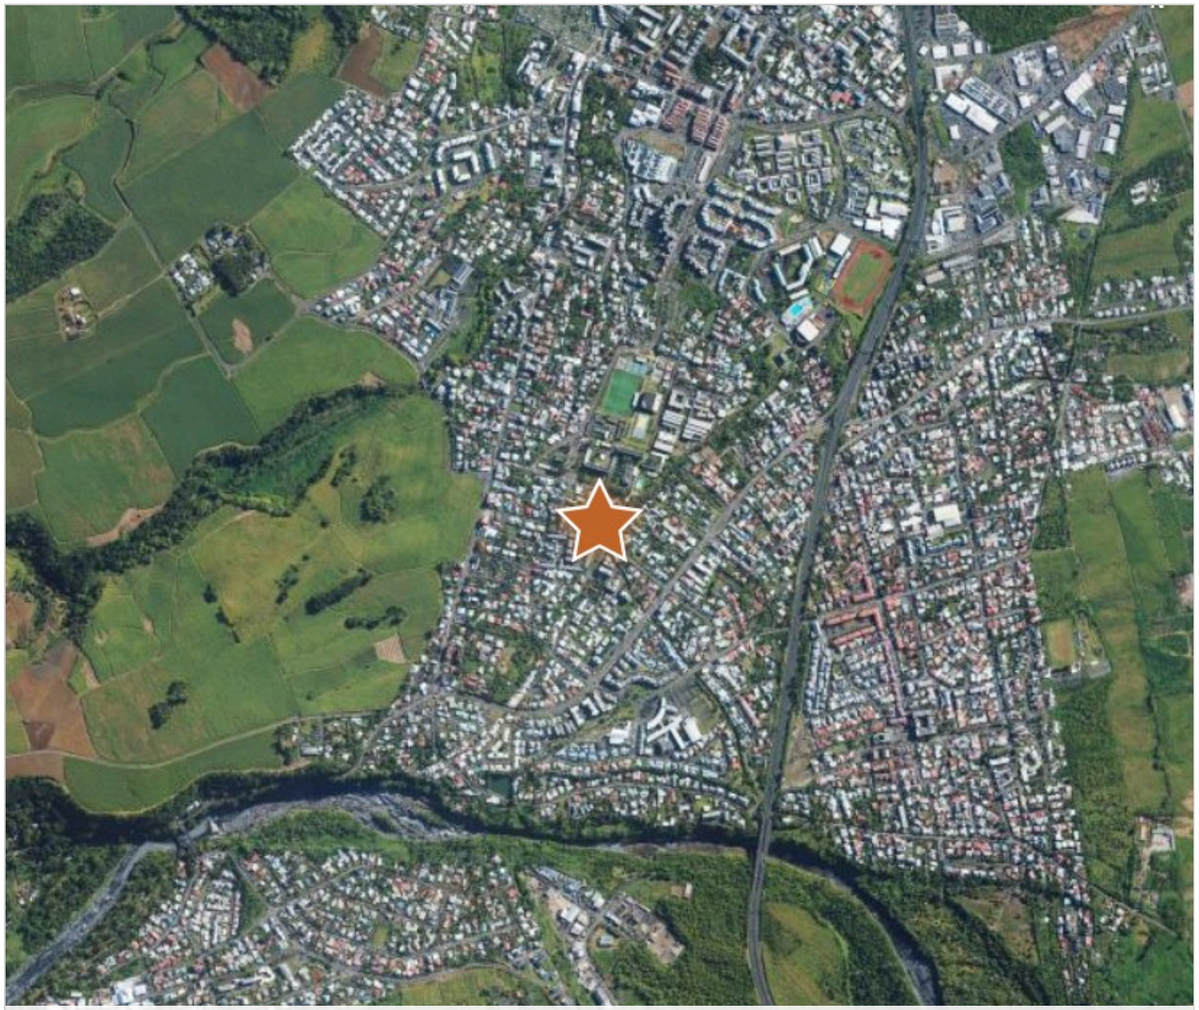


Situation — commune de Saint-André, orthophoto IGN (Géoplateforme) · parcelle BH 513 (étoile)

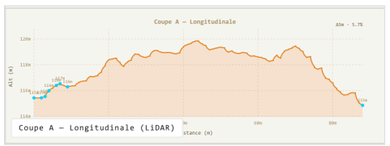

Profil longitudinal LiDAR (Δ 5 m · 5,7 %)

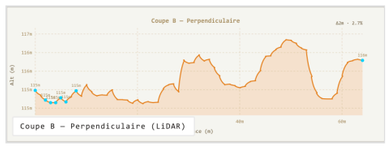

Profil transversal LiDAR (Δ 2 m · 2,7 %)

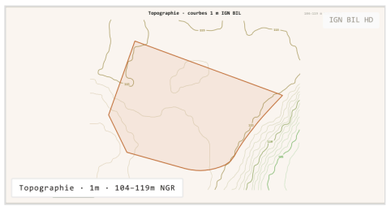

Courbes 1 m — IGN RGE ALTI

LE SITE

Friche arborée au cœur du quartier Mille Roches (NPNRU), bordée au sud et à l'est par le chemin Mille Roches, au nord par un tissu de cases et de petits collectifs, à l'ouest par le lot A cédé à la SIDR. Plateau quasi plan entre **114,3 et 116,7 m NGR** ; la limite est surplombe une ravine (talus, bande B2u). Climat de la côte au vent : **alizés d'est**, pluviométrie ≈ **2 365 mm/an**.

RISQUES — PPRN SAINT-ANDRÉ (BRGM 2026)

- **B3 — inondation, prescriptions** : planchers calés au-dessus de la cote de référence ; **pas de sous-sol** ; clôtures transparentes hydrauliquement.
- **B2u — inondation + mouvement de terrain** : couloir de la ravine en limite est, laissé libre de construction (+ 1 m).
- Zone rouge **R1** au sud-est, hors parcelle.

PLU APPROUVÉ LE 02/07/2025 — ZONE UE

> **Point bloquant** — en Ue, la sous-destination **« hébergement » est interdite**. Un FJT relève de l'hébergement (« foyers de travailleurs », art. R151-28). Le projet — comme l'opération SIDR voisine — suppose une **évolution du PLU** (modification ou déclaration de projet, reclassement en Ub), ou une qualification en équipement d'intérêt collectif à faire valider par le service instructeur.

Règles Ue retenues : hauteur **16 m** (R+3 conforme : faîtage ≈ 13,9 m au-dessus du RDC) ; recul **3 m** sur voie ; **4 m** sur limites séparatives et de fond ; pas de blanc en paroi ni de tôle non peinte.

PROGRAMME (NOTE KONSEYALI DU 06/10, VALIDÉE MLE LE 07/10)

- FJT : **60 logements** — 50 T1 de 20 m², 7 T1 bis de 30 m², 3 T2 de 46 m², produit LLTS
- Communs FJT : salle d'activités et cuisine, buanderie, sanitaires, bureaux de coordination, hall, locaux vélos et poubelles
- **Pôle administratif MLE** 151 m² et **micro-crèche** 12 places 100 m² + 20 m² extérieurs — réintégrés dans l'assiette
- R+3 maximum ; stationnement 1 place / 3 logements + besoins MLE et crèche



Assiette FJT (orange) — partie est de BH 513, après cession du lot A à la SIDR (à l'ouest)

CE QUI A CHANGÉ DEPUIS L'IND 0

L'ind 0 supposait le lot SIDR en bande nord. Le permis de construire de la SIDR (« Opération Sirandane », NKN architecture, déposé le 30/09/2026 — 25 LLS R+3, 935 m² d'emprise) fixe le **lot A à l'ouest** : limite nord 33,86 m, ouest 46,70 m, est 62,50 m (nouvelle limite), sud 24,87 + 16,05 m sur le chemin.


ASSIETTE RETENUE

- Lot A SIDR ≈ 2 005 m² (reconstitué depuis les cotes du PC).
- **Assiette FJT ≈ 2 965 m²** : façade sud sur le chemin Mille Roches, est sur le chemin et la ravine (B2u), nord sur les cases.
- Bâtiments SIDR C et D (R+3, ≈ 12,5 m) à 3 m de la limite commune : vis-à-vis pris en compte dans l'implantation.
- Les eaux usées de la SIDR sortent à l'angle nord-est du lot A : **servitude de réseaux** le long de la limite nord de l'assiette FJT.


> **À confirmer** avec la SEMAC, NKN et le géomètre : plan de division (non transmis), tracé de la servitude, cote de référence PPRN.

ENVELOPPE CONSTRUCTIBLE FJT

Assiette FJT	**2 965 m²**
Reculs Ue : voie 3 m · limites 4 m	—
Hors B2u (+1 m)	—
Enveloppe constructible	**2 059 m²**

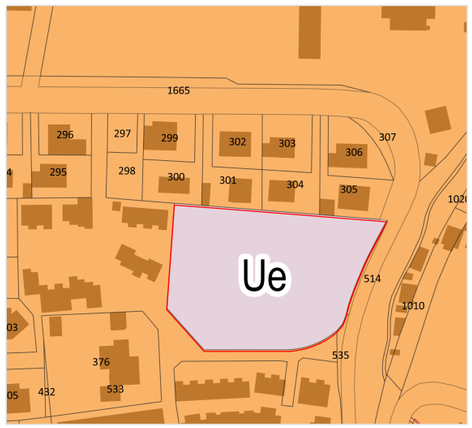

PLU 2025 — zonage Ue de BH 513 · planche n°2

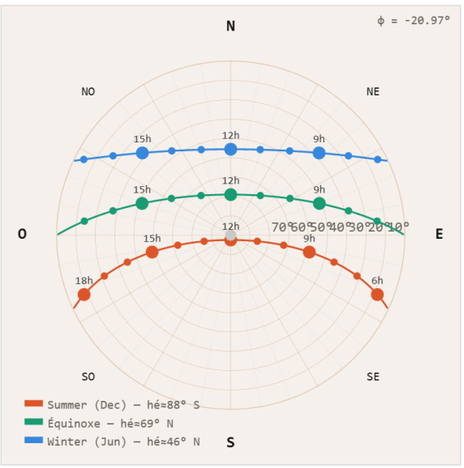

Héliodon TERLAB — ensoleillement de l'assiette



Scénario retenu — plan masse coté (BVE)

PRINCIPE

Deux lames R+3 à coursives, orientées nord-nord-est / sud-sud-ouest, tenues à distance du lot SIDR, autour d'une **cour plantée** réservée aux résidents. Le **stationnement** est regroupé en haut de parcelle, à 1,5 m des limites, desservi depuis le chemin à l'est ; les deux lames se prolongent au-dessus de ce parking (A' et B', sur poteaux) jusqu'à leurs escaliers et ascenseurs, reliés par une passerelle.

- **Bât. A** (est) : micro-crèche au RDC (entrée à l'est, jardin de 20 m²), services FJT et salle collective au sud ; logements aux étages.
- **Bât. B** (ouest) : bureaux FJT au nord et **pôle administratif MLE** au sud (accueil du public sur le chemin) ; logements aux étages.
- Entrées séparées : résidence à l'est près de l'accès véhicules, crèche à l'est, public MLE au sud-ouest ; partie clôturée MLE + services FJT au RDC.
- RDC calé au-dessus du terrain naturel (B3), sans sous-sol ; toitures 4 pans à 22°, débords 0,80 m.

CHIFFRES CLÉS

Assiette FJT (après division SIDR)	**2 965 m²**
Enveloppe constructible (reculs 3 / 4 / 4 m, hors B2u)	**2 059 m²**
Logements	**60 (50 T1 · 7 T1 bis · 3 T2)**
Surface habitable (SHAB)	**1 401 m²**
Locaux annexes (SU) : communs FJT, micro-crèche, pôle MLE	**484 m²**
Surface de plancher	**2 299 m² (cible 2 234)**
Emprise bâtie	**1 002 m² (34 %)**
Hauteur	**R+3 · faîtage 129,27 à 129,75 m NGR (≈ 13,9 m)**
Stationnement	**35 pl. pour 34 (FJT 21, Pôle MLE 7, Micro-crèche 6)**
Arbres	**13 abattus · 21 replantés**



Depuis l'accès véhicules — stationnement sous A' et B' (IA, non contractuelle)



La cour entre les lames (IA, non contractuelle)



LÉGENDE

Limites et bâti

- assiette FJT (2 965 m²)
- enveloppe constructible
- lames A et B, R+3, toiture 4 pans
- prolongements A' et B' sur poteaux
- stationnement (35 pl.)
- lot SIDR (PC NKN)
- B2u (+1 m), inconstructible
- arbre abattu (13)

Espaces extérieurs par fonction

- Cour, jardin commun
- Équipement, salle collective
- Crèche, école (cour)

Clôtures (projet BVE)

- grillage doublé d'une haie · 43 ml
- grille sur bahut doublée d'une haie · 102 ml
- portillon (4)
- portail battant, accès véhicules (1)

Accès

- accès véhicules
- entrées piétonnes : résidents, FJT, crèche, public MLE
- allées piétonnes, 1,4 m de large

Orthophoto IGN (Géoplateforme, 2026) · repère maquette, RGR92 UTM 40S · échelle 1/500 sur A3 (barre graphique : 20 m) · lames et prolongements sur poteaux d'après la sonde BVE · voisins SIDR d'après le PC (NKN, sept. 2026) · clôtures d'après le projet BVE · fonctions et teintes des espaces : catalogue USAGES de BVE.




Rez-de-chaussée (± 0,00 : 115,41 à 115,89 m NGR) — communs FJT, micro-crèche, pôle MLE, salle collective ; parking sous A' et B'



Étage courant, R+1 (+ 3,00) — logements en travées, coursives sur la cour

Appartement type T1s · Bât. A · R+1

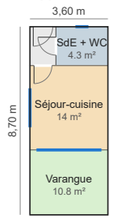


pièce	aire	minimum	dim.	état
Entrée	2,16 m²	—	1,20 / 1,2	ok
SdE + WC	4,32 m²	3,0 m²	1,80 / 1,5	ok
Séjour-cuisine	14,04 m²	14,0 m²	3,60 / 2,4	ok
Varangue	10,80 m²	—	—	—

SHAB 20,52 m² pour une cible de 20 m² (+2.6 %)
conforme aux minima

T1 (cible 20 m²)

Appartement type T1bis · Bât. B · R+3

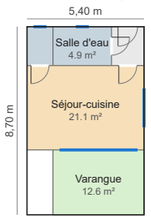


pièce	aire	minimum	dim.	état
WC	2,16 m²	—	1,20 / 0,9	ok
Salle d'eau	4,86 m²	3,0 m²	1,80 / 1,5	ok
Entrée	2,70 m²	—	1,50 / 1,2	ok
Séjour-cuisine	21,06 m²	14,0 m²	3,90 / 2,4	ok
Varangue	12,60 m²	—	—	—

SHAB 30,78 m² pour une cible de 30 m² (+2.6 %)
conforme aux minima

T1 bis

Appartement type T2 · Bât. A · R+1

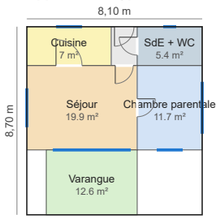


pièce	aire	minimum	dim.	état
Cuisine	7,02 m²	4,5 m²	1,80 / 1,8	ok
Entrée	2,16 m²	—	1,20 / 1,2	ok
SdE + WC	5,40 m²	3,0 m²	1,80 / 1,5	ok
Séjour	19,89 m²	14,0 m²	3,90 / 2,4	ok
Chambre parentale	11,70 m²	9,0 m²	3,00 / 2,4	ok
Varangue	12,60 m²	—	—	—

SHAB 46,17 m² pour une cible de 46 m² (+0.4 %)
conforme aux minima

T2 (cible 46 m²)

Plans de la planche BVE, recadrés sur les bâtiments (échelle ≈ 1/250) ; trame 0,30 m ; profondeur utile 5,70 m ; varangue 1,20 m sur l'extérieur pour chaque logement.

Coupe AA — transversale au droit des deux lames (regard vers le nord-nord-est) · lot SIDR à gauche (ouest), chemin Mille Roches à droite (est)

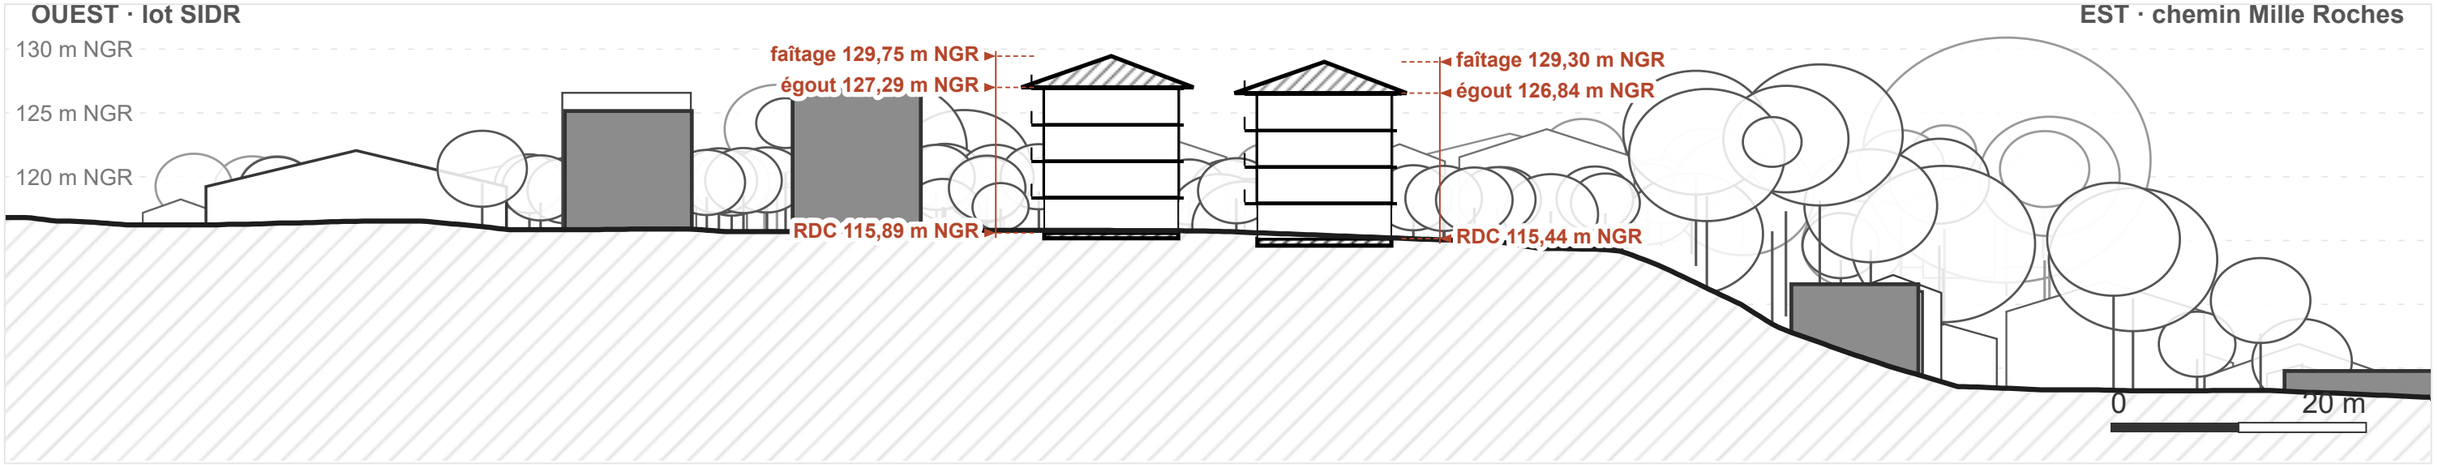

Façade urbaine est — depuis le chemin Mille Roches (regard vers l'ouest-nord-ouest) · lames A et B en premier plan, A' et B' sur poteaux au fond




Façade urbaine sud — depuis le chemin Mille Roches (regard vers le nord)



Terrain naturel : maillage de la maquette (IGN RGE ALTI / LiDAR HD), trait fort · bâti existant : IGN BD TOPO (hauteurs mesurées), voisins SIDR d'après le PC, trait gris selon la profondeur · arbres : LiDAR HD, 13 abattus ôtés · projet : RDC 115,41 à 115,89 m NGR, niveaux de 2,85 m, toitures 4 pans 22°, débord 0,80 m · cotes en m NGR · façades en élévation au trait noir et blanc, projetées depuis le GLB détaillé de la maquette (arêtes vives seulement ; vitrages en gris, toitures hachurées dans le sens de la pente).

Coupe territoriale des Hauts à l'océan (≈ 10 km, axe OSO → ENE) — échelle ≈ 1/25 000, hauteurs ×3

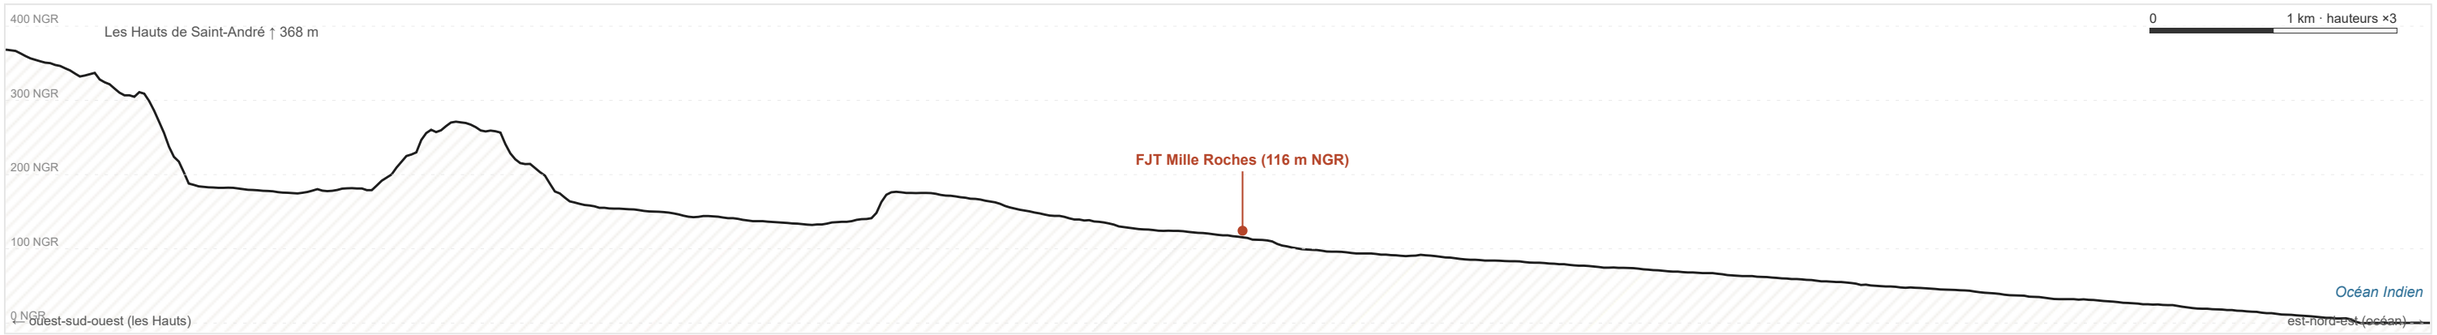

LECTURE

Mille Roches est posé à mi-pente (≈ 116 m NGR) entre les Hauts de Saint-André et le littoral, sur le rebord d'un plateau ; à l'est un talus d'une dizaine de mètres (ravine, B2u) descend vers la plaine de la Rivière du Mât.

Les deux lames R+3 (faîtage 129,27 à 129,75 m NGR) restent dans l'épannelage des collectifs voisins, dont les bâtiments SIDR R+3, et sous la ligne des grands arbres du talus.

CONSÉQUENCES POUR LE PROJET

- Conserver la **lisière arborée du talus** (B2u non bâtie) : filtre visuel et hydraulique.
- 13 arbres abattus, 21 replantés (cour, abords du parking).
- Eaux pluviales gérées à la parcelle avant le talus — pas de rejet direct dans la pente.



Vue aérienne depuis le sud-ouest — les deux lames, le stationnement en haut de parcelle, la cour plantée



Depuis le chemin Mille Roches — clôture sur voie, entrée piétonne



La cour entre les lames — coursives, passerelles, clôture ajourée de la cour

Vues de la maquette 3D BVE (IGN BD TOPO, RGE ALTI, LiDAR HD, orthophoto IGN), volumétries indicatives. Perspectives d'ambiance générées par IA (Leonardo, Nano Banana) à partir des vues de base de la maquette détaillée, contrôlées avant génération (baies, varangues, coursives, toitures 4 pans, RDC réel, clôtures) : images **non contractuelles**, matériaux et ambiance indicatifs.

PROGRAMME PAR BÂTIMENT ET PAR NIVEAU

Bât.	Niveau	Destination	T1	T1 bis	T2	SHAB m²	Annexes SU m²	SDP m²
Bât. A	RDC	Communs FJT · Extérieurs · Micro-crèche	—	—	—	—	241,0	293,9
Bât. A	R+1	Logements · Communs FJT	5	—	1	145,1	20,0	201,3
Bât. A	R+2	Logements	6	—	1	169,3	—	206,5
Bât. A	R+3	Logements	6	—	1	169,3	—	206,5
Total Bât. A			**17**	**0**	**3**	**483,7**	**261,0**	**908,2**
Bât. B	RDC	Communs FJT · Pôle admin MLE	—	—	—	—	223,0	272,0
Bât. B	R+1	Logements	7	—	—	143,6	—	175,1
Bât. B	R+2	Logements	7	—	—	143,6	—	175,1
Bât. B	R+3	Logements	5	1	—	133,4	—	162,7
Total Bât. B			**19**	**1**	**0**	**420,6**	**223,0**	**784,9**
Bât. A' (sur parking)	RDC	Rez-de-chaussée sur poteaux — stationnement	—	—	—	—	—	—
Bât. A' (sur parking)	R+1	Logements	3	—	—	64,9	—	79,1
Bât. A' (sur parking)	R+2	Logements	3	—	—	64,9	—	79,1
Bât. A' (sur parking)	R+3	Logements	2	—	—	43,3	—	52,8
Total Bât. A' (sur parking)			**8**	**0**	**0**	**173,1**	**—**	**211,0**
Bât. B' (sur parking)	RDC	Rez-de-chaussée sur poteaux — stationnement	—	—	—	—	—	—
Bât. B' (sur parking)	R+1	Logements	2	2	—	108,0	—	131,7
Bât. B' (sur parking)	R+2	Logements	2	2	—	108,0	—	131,7
Bât. B' (sur parking)	R+3	Logements	2	2	—	108,0	—	131,7
Total Bât. B' (sur parking)			**6**	**6**	**0**	**324,0**	**—**	**395,1**
TOTAL — 60 logements			**50**	**7**	**3**	**1401,4**	**484,0**	**2299,2**

SYNTHÈSE

Logements	60	50 T1 + 7 T1 bis + 3 T2
Surface habitable (SHAB)	1401,4 m²	moyenne 23,4 m² / logement
Locaux annexes (SU)	484,0 m²	communs FJT, micro-crèche 100 m², pôle MLE 151 m²
Surface de plancher	2299,2 m²	cible 2 234 m² (+3 %)
Ratio SHAB / SDP	0,61	coursives extérieures hors SDP
Emprise bâtie	1 002 m²	34 % de l'assiette (CES maximal 0.6)
Stationnement	35 pl.	besoin 34 (FJT 21, Pôle MLE 7, Micro-crèche 6) · haut de parcelle 23 · allée 3 · chemin 3 · autres 6
Arbres	13 / 21	abattus / replantés
Clôture — grillage doublé d'une haie	43 ml	4 tronçon(s)
Clôture — grille sur bahut doublée d'une haie	102 ml	1 tronçon(s)
Ouvertures	5	1 battant · 4 portillon

Type	Nombre	Surface cible	SHAB cible cumulée
T1	50	20 m²	1 000 m²
T1 bis	7	30 m²	210 m²
T2	3	46 m²	138 m²

SHAB : surface habitable ; SU annexes : communs FJT, micro-crèche, pôle MLE ; SDP : pré-dimensionnement ±10 % (coursives hors SDP). Source : sonde BVE « opération collective », projet MGA-26-04.

POINTS DE VIGILANCE

1. **PLU 2025 — zone Ue** : l'hébergement (FJT) y est **interdit**. Évolution du PLU à engager avec la Ville, en commun avec l'opération SIDR.
2. **Assiette** : plan de division et servitude de réseaux à obtenir (SEMAC, NKN, géomètre).
3. **PPRN** : cote de référence B3 à obtenir ; l'accès véhicules traverse la bande B2u : à faire valider.
4. **Stationnement** : 35 places pour un besoin estimé de 34 (MLE et crèche à confirmer avec l'exploitant).
5. **Programme** : salle collective de 75 m² à confirmer ; place du pôle MLE et de la micro-crèche validée sur le principe.
6. **Topographie** : relevé géomètre à commander ; l'étude repose sur le LiDAR HD IGN (≈ 10 cm).
7. **Alertes de la sonde BVE** : réserve de stationnement sur une servitude (73.47 m²) : admis, à confirmer.
8. **Rampes à 5 %** (entrée est : 16,2 m, 1 palier ; crèche : 11,4 m) : à confirmer avec le terrassement.
9. **Circulations** : 12 passage(s) de raccord coursive / palier sous la largeur libre de 1,20 m (minimum 1,00 m) : à élargir ou à valider avec le bureau de contrôle.

SUITE PROPOSÉE

- Réunion Ville / SEMAC / SIDR sur l'évolution du PLU.
- Plans types T1, T1 bis et T2 calés sur le programme.
- Estimation des travaux et montage (LLTS, FSE, bonus EPFR).
- Perspectives d'ambiance contrôlées pour la présentation aux élus.



LÉGENDE

Limites et bâti

- assiette FJT (2 965 m²)
- enveloppe constructible
- lames A et B, R+2, toiture 4 pans
- prolongements A' et B' sur poteaux
- stationnement (26 pl.)
- lot SIDR (PC NKN)
- B2u (+1 m), inconstructible
- arbre abattu (13)

Espaces extérieurs par fonction

- Cour, jardin commun

Clôtures (projet BVE)

- grille sur bahut doublée d'une haie · 102 ml
- portillon (2)
- portail battant, accès véhicules (1)

Accès

- accès véhicules
- entrées piétonnes : résidents, FJT
- allées piétonnes, 1,4 m de large

Orthophoto IGN (Géoplateforme, 2026) · repère maquette, RGR92 UTM 40S · échelle 1/500 sur A3 (barre graphique : 20 m) · lames R+2, parking du haut seul d'après la sonde BVE · voisins SIDR d'après le PC (NKN, sept. 2026) · clôtures d'après le projet BVE · fonctions et teintes des espaces : catalogue USAGES de BVE.

VARIANTE R+2 : PROGRAMME PAR BÂTIMENT ET PAR NIVEAU

Bât.	Niveau	Destination	T1	T1 bis	T2	SHAB m²	Annexes SU m²	SDP m²
Bât. A	RDC	Logements · Communs FJT · Extérieurs	3	2	—	123,1	141,0	322,1
Bât. A	R+1	Logements · Communs FJT	5	1	—	131,9	20,0	185,2
Bât. A	R+2	Logements	6	1	—	153,9	—	187,7
Total Bât. A			**14**	**4**	**0**	**408,9**	**161,0**	**695,0**
Bât. B	RDC	Logements · Communs FJT	3	—	1	107,7	72,0	219,1
Bât. B	R+1	Logements	6	—	1	169,3	—	206,5
Bât. B	R+2	Logements	7	—	—	143,6	—	175,1
Total Bât. B			**16**	**0**	**2**	**420,6**	**72,0**	**600,7**
Bât. A' (sur parking)	RDC	Rez-de-chaussée sur poteaux — stationnement	—	—	—	—	—	—
Bât. A' (sur parking)	R+1	Logements	3	—	—	64,9	—	79,1
Bât. A' (sur parking)	R+2	Logements	2	—	—	43,3	—	52,8
Total Bât. A' (sur parking)			**5**	**0**	**0**	**108,2**	**—**	**131,9**
Bât. B' (sur parking)	RDC	Rez-de-chaussée sur poteaux — stationnement	—	—	—	—	—	—
Bât. B' (sur parking)	R+1	Logements	3	1	—	97,2	—	118,5
Bât. B' (sur parking)	R+2	Logements	3	1	—	97,2	—	118,5
Total Bât. B' (sur parking)			**6**	**2**	**0**	**194,4**	**—**	**237,0**
TOTAL — 49 logements			**41**	**6**	**2**	**1132,1**	**233,0**	**1664,6**

SHAB : surface habitable ; SU annexes : communs FJT et locaux techniques ; SDP : pré-dimensionnement ±10 % (coursives hors SDP). Source : sonde BVE « opération collective », projet MGA-26-04.

SCÉNARIO RETENU ET VARIANTE : COMPARAISON


Critère	Scénario retenu R+3	Variante R+2	Écart
Niveaux et logements			
Hauteur des lames (R+n)	3	2	**−1**
Logements	60	49	**−11**
dont T1	50	41	**−9**
dont T1 bis	7	6	**−1**
dont T2	3	2	**−1**
Logements au RDC	0	9	**+9**
Surfaces			
Surface habitable (SHAB)	1 401 m²	1 132 m²	**−269 m²**
Surface de plancher (SDP)	2 299 m²	1 665 m²	**−635 m²**
Emprise bâtie	1 002 m²	1 021 m²	**+19 m²**
Locaux annexes (SU)	484 m²	233 m²	**−251 m²**
— Communs FJT	214 m²	214 m²	**=**
— Pôle administratif MLE	151 m²	0 m²	**−151 m²**
— Micro-crèche	100 m²	0 m²	**−100 m²**
— Locaux vélos et poubelles	19 m²	19 m²	**=**
Stationnement			
Places	35	26	**−9**
Besoin estimé	34	17	**−17**
Places en excédent	1	9	**+8**
Hauteurs (m NGR)			
Faîtage des lames	129,27 à 129,75	126,47 à 126,95	**−2,8 m**
Hauteur du faîtage au-dessus du RDC	13,9 m	11,1 m	**−2,8 m**
Espaces extérieurs (clôtures BVE)			
Espaces extérieurs de l'assiette	1 962 m²	1 944 m²	**−18 m²**
— cour, jardin commun	1 146 m²	1 944 m²	**+798 m²**
— équipement (MLE, services)	751 m²	0 m²	**−751 m²**
— cour de la crèche	65 m²	0 m²	**−65 m²**
Nombre d'espaces	3	1	**−2**

CE QUI CHANGE


- **Un niveau de moins** : R+2 au lieu de R+3, faîtage à 126,47–126,95 m NGR contre 129,27–129,75 (11,1 m au-dessus du RDC contre 13,9).
- **Pôle MLE et micro-crèche retirés** : 251 m² de locaux annexes en moins (MLE 151 m², crèche 100 m²) et la cour de la crèche (65 m²) ; les annexes ne sont plus que les communs FJT et les locaux techniques (233 m²).
- **Logements au RDC** : 9 logements au rez-de-chaussée, à côté des communs FJT.
- **Parking du bas supprimé** : 9 places en moins (26 contre 35), toutes en haut de parcelle (23 sur la réserve + 3 le long de l'allée) ; une seule cour des résidents de 1 944 m².
- Résultat : **49 logements** (41 T1, 6 T1 bis, 2 T2) au lieu de 60, SHAB 1 132 m² (1 401 m²), SDP 1 665 m² (2 299 m²).

CE QUI PLAFONNE


Le **stationnement n'est pas limitant** : 26 places pour un besoin de 17 (9 en excédent). Ce sont **l'enveloppe constructible** (2 059 m² pour une assiette de 2 965 m², emprise bâtie 1 021 m², soit 50 % de l'enveloppe) et **la longueur des lames** (Bât. A 31,5 m, Bât. B 29,7 m, profondeur 10,5 m) qui bornent le nombre de logements (reculs 3 / 4 / 4 m, hors B2u).

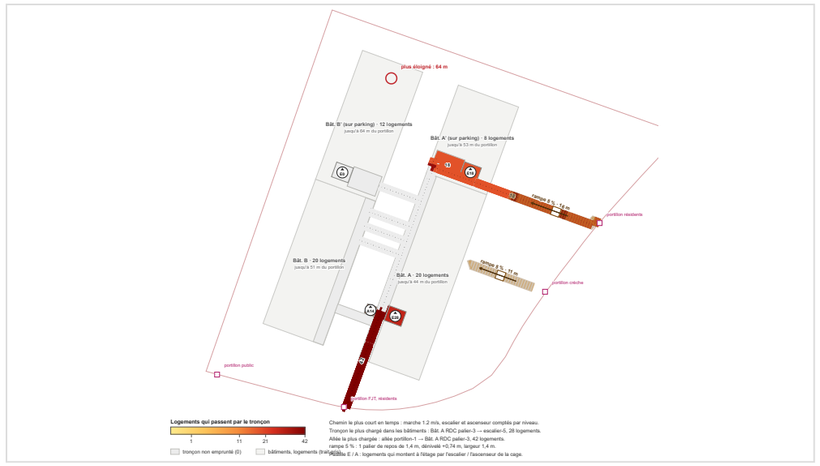

Plan de masse — scénario retenu R+3, chemin le plus court

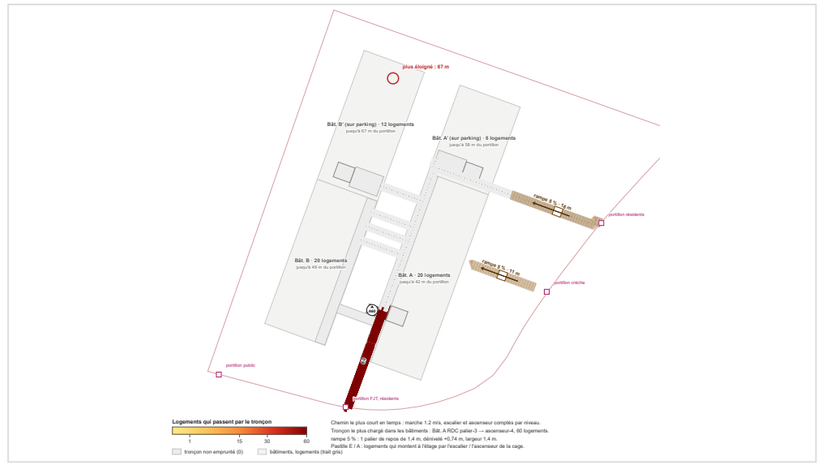

Plan de masse — scénario retenu R+3, parcours PMR (ascenseur seul)

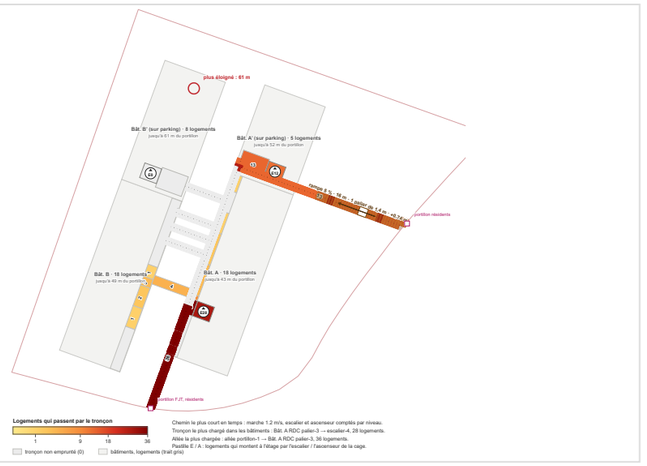

Plan de masse — variante R+2, chemin le plus court



Étage R+1 — retenu, chemin le plus court



Étage R+1 — retenu, parcours PMR



Étage R+1 — variante R+2

Retenu R+3 — 60 logements, chemin le plus court			
Répartition par entrée (distance et temps maximaux portillon → porte)			
portillon FJT, résidents	42 logements	53,3 m	1 min 28
portillon résidents	18 logements	64,1 m	1 min 38
Distance maximale	64,1 m, Bât. B' (sur parking) R+1 t-1-01 (1 min 08)		
Tronçon le plus chargé	allée portillon-1 → Bât. A RDC palier-3 : 42 logements ; dans les bâtiments : Bât. A RDC palier-3 → escalier-5, 28		
Ascenseur	ascenseur **requis** au-delà de R+2, 1 présent en Bât. A		
Continuité	**conforme** : 60 logement(s) atteints depuis un portillon par un cheminement continu (allées, halls, coursives, escaliers, passerelles).		
Largeur de raccord coursive / palier	**avertissement** : 12 passage(s) sous 1,20 m (minimum 1,00 m)		

Retenu R+3 — parcours PMR	
Parcours PMR : ascenseur seul pour les étages	
Entrée de référence	portillon FJT (sud) : 60 logements, 67,3 m au plus loin, 1 min 40
Distance maximale	67,3 m, Bât. B' (sur parking) R+2 t-2-01 (1 min 32)
Flux de l'ascenseur	60 logements au départ du RDC, puis 40, 19 (R+1, R+2, R+3)
Rampe, entrée est (résidents)	16,2 m, pente 5 %, dénivelé +0,74 m, 1 palier(s) de repos de 1,4 m, largeur 1,4 m (pente du terrain 10,7 %)
Rampe, crèche	11,4 m, pente 5 %, dénivelé +0,50 m, 1 palier(s) de repos de 1,4 m, largeur 1,4 m (pente du terrain 8,4 %)
Compromis portillon	portillon est inchangé : dénivelé net 1,42 m, rampe de 31,1 m, 2 palier(s) ; la meilleure position, déplacée de 9,0 m, ramènerait le dénivelé à 1,25 m (rampe de 27,9 m)
Rampes (PMR_PENTES)	**conforme** : 3 allée(s) résidents à plus de 8 % : rampe à 5 %, 16 m, 1 palier(s) de repos. Allées résidents : pente maximale 10.7 %, 3 allée(s) entre 5 et 8 % (rampe à paliers de repos).

Variante R+2 — 49 logements (sans ascenseur : pas de parcours PMR)			
Répartition par entrée (distance et temps maximaux portillon → porte)			
portillon FJT, résidents	36 logements	52,7 m	1 min 11
portillon résidents	13 logements	61,5 m	1 min 21
Distance maximale	61,5 m, Bât. B' (sur parking) R+1 t-1-01 (1 min 06)		
Tronçon le plus chargé	allée portillon-1 → Bât. A RDC palier-3 : 36 logements ; dans les bâtiments : Bât. A RDC palier-3 → escalier-4, 28		
Ascenseur	ascenseur **facultatif** jusqu'à R+2 inclus, 0 présent		
Continuité	**conforme** : 49 logement(s) atteints depuis un portillon par un cheminement continu (allées, halls, coursives, escaliers, passerelles).		
Largeur de raccord coursive / palier	**avertissement** : 8 passage(s) sous 1,20 m (minimum 1,00 m)		

Lecture. L'entrée PMR de référence est l'entrée FJT, au sud, à 17,5 m du portillon pour l'ascenseur ; elle dessert les 60 logements par l'ascenseur seul (distance maximale 67,3 m, contre 64,1 m au plus court). L'ascenseur est dans le noyau du Bât. A, en saillie sur la cour. Deux entrées desservent les logements au plus court, le portillon FJT, au sud, et le portillon résidents, à l'est ; le scénario retenu les répartit en 42 et 18 logements, la variante R+2 en 36 et 13. L'entrée est est rendue accessible par une rampe à 5 % de 16,2 m, avec 1 palier de repos. Le chemin de la crèche (rampe de 11,4 m) et celui du public MLE restent à part des chemins des résidents. Ascenseur : requis en R+3 (1 présent), facultatif en R+2 (0 présent). Les raccords palier / coursive sous 1,20 m de large sont signalés dans les tableaux.