

Image d'ambiance générée par IA à partir de la maquette 3D — non contractuelle

semac
SOCIÉTÉ D'ÉCONOMIE MIXTE
D'AMÉNAGEMENT ET DE CONSTRUCTION

Étude de faisabilité · capacité


Foyer de Jeunes Travailleurs

Mille Roches, Saint-André


ind 1 — scénario retenu · document de travail
OCTOBRE 2026

Adresse	573 chemin Mille Roches, 97440 Saint-André
Cadastre	BH 513 pour partie — partie est, ≈ 2 965 m²
Programme	FJT 60 logements LLTS · communs · pôle administratif MLE · micro-crèche 12 places — exploitant MLE
Zone PLU	**Ue** — équipements (PLU approuvé le 02/07/2025) · hébergement interdit : évolution du PLU requise
PPRN	B3 inondation · B2u en limite est
Dossier	MGA-26-04


Mathias Giraud Architecture mgA.

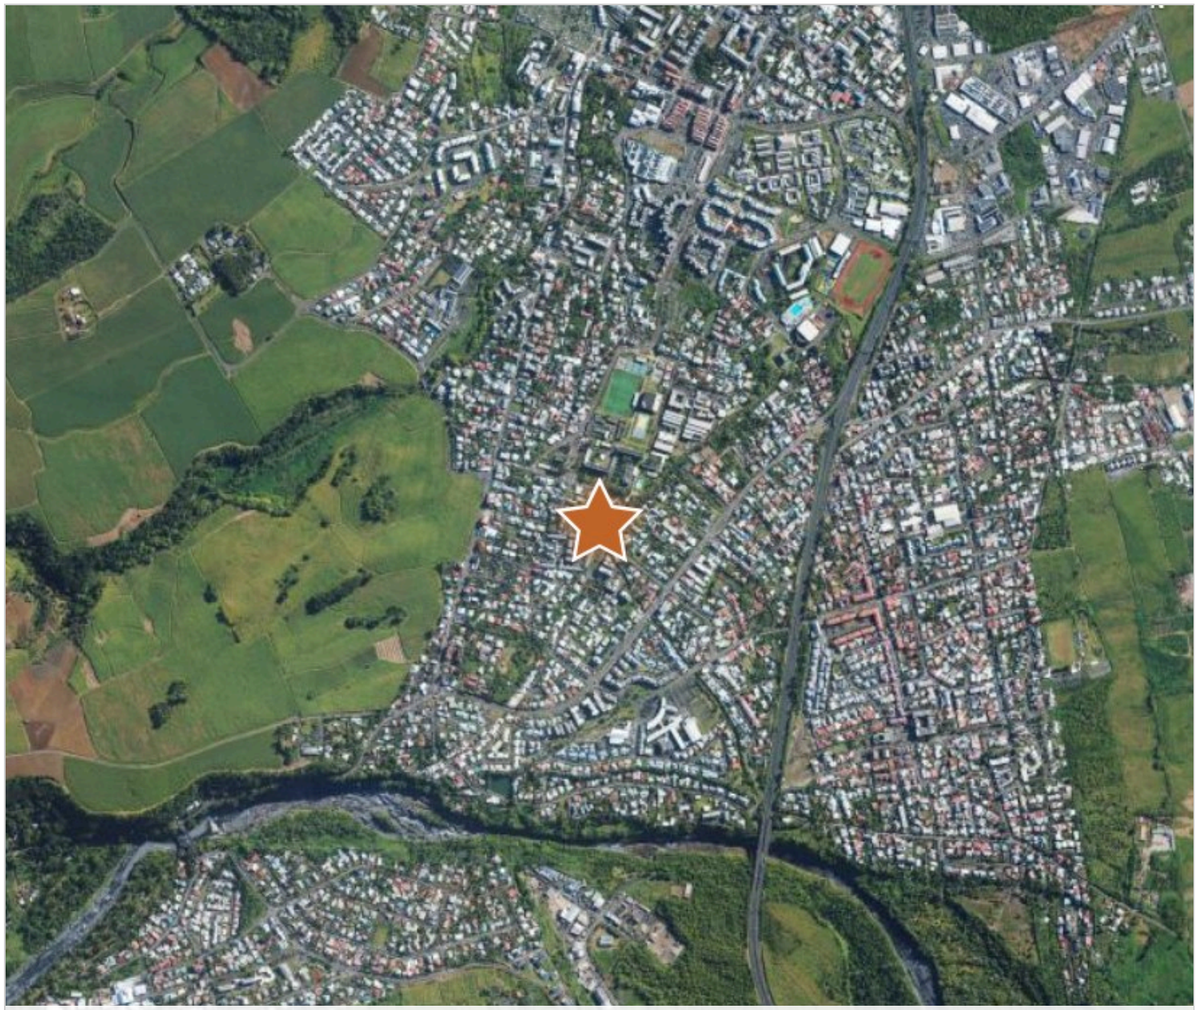


Situation — commune de Saint-André, orthophoto IGN (Géoplateforme) · parcelle BH 513 (étoile)

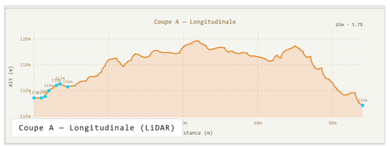

Profil longitudinal LiDAR (Δ 5 m · 5,7 %)

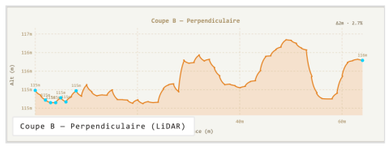

Profil transversal LiDAR (Δ 2 m · 2,7 %)

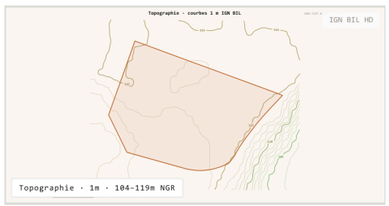

Courbes 1 m — IGN RGE ALTI

LE SITE

Friche arborée au cœur du quartier Mille Roches (NPNRU), bordée au sud et à l'est par le chemin Mille Roches, au nord par un tissu de cases et de petits collectifs, à l'ouest par le lot A cédé à la SIDR. Plateau quasi plan entre **114,3 et 116,7 m NGR** ; la limite est surplombe une ravine (talus, bande B2u). Climat de la côte au vent : **alizés d'est**, pluviométrie ≈ **2 365 mm/an**.

RISQUES — PPRN SAINT-ANDRÉ (BRGM 2026)

- **B3 — inondation, prescriptions** : planchers calés au-dessus de la cote de référence ; **pas de sous-sol** ; clôtures transparentes hydrauliquement.
- **B2u — inondation + mouvement de terrain** : couloir de la ravine en limite est, laissé libre de construction (+ 1 m).
- Zone rouge **R1** au sud-est, hors parcelle.

PLU APPROUVÉ LE 02/07/2025 — ZONE UE

> **Point bloquant** — en Ue, la sous-destination **« hébergement » est interdite**. Un FJT relève de l'hébergement (« foyers de travailleurs », art. R151-28). Le projet — comme l'opération SIDR voisine — suppose une **évolution du PLU** (modification ou déclaration de projet, reclassement en Ub), ou une qualification en équipement d'intérêt collectif à faire valider par le service instructeur.

Règles Ue retenues : hauteur **16 m** (R+3 conforme : faîtage ≈ 13,9 m au-dessus du RDC) ; recul **3 m** sur voie ; **4 m** sur limites séparatives et de fond ; pas de blanc en paroi ni de tôle non peinte.

PROGRAMME (NOTE KONSEYALI DU 06/10, VALIDÉE MLE LE 07/10)

- FJT : **60 logements** — 50 T1 de 20 m², 7 T1 bis de 30 m², 3 T2 de 46 m², produit LLTS
- Communs FJT : salle d'activités et cuisine, buanderie, sanitaires, bureaux de coordination, hall, locaux vélos et poubelles
- **Pôle administratif MLE** 151 m² et **micro-crèche** 12 places 100 m² + 20 m² extérieurs — réintégrés dans l'assiette
- R+3 maximum ; stationnement 1 place / 3 logements + besoins MLE et crèche



Assiette FJT (orange) — partie est de BH 513, après cession du lot A à la SIDR (à l'ouest)

CE QUI A CHANGÉ DEPUIS L'IND 0

L'ind 0 supposait le lot SIDR en bande nord. Le permis de construire de la SIDR (« Opération Sirandane », NKN architecture, déposé le 30/09/2026 — 25 LLS R+3, 935 m² d'emprise) fixe le **lot A à l'ouest** : limite nord 33,86 m, ouest 46,70 m, est 62,50 m (nouvelle limite), sud 24,87 + 16,05 m sur le chemin.


ASSIETTE RETENUE

- Lot A SIDR ≈ 2 005 m² (reconstitué depuis les cotes du PC).
- **Assiette FJT ≈ 2 965 m²** : façade sud sur le chemin Mille Roches, est sur le chemin et la ravine (B2u), nord sur les cases.
- Bâtiments SIDR C et D (R+3, ≈ 12,5 m) à 3 m de la limite commune : vis-à-vis pris en compte dans l'implantation.
- Les eaux usées de la SIDR sortent à l'angle nord-est du lot A : **servitude de réseaux** le long de la limite nord de l'assiette FJT.


> **À confirmer** avec la SEMAC, NKN et le géomètre : plan de division (non transmis), tracé de la servitude, cote de référence PPRN.

ENVELOPPE CONSTRUCTIBLE FJT

Assiette FJT	**2 965 m²**
Reculs Ue : voie 3 m · limites 4 m	—
Hors B2u (+1 m)	—
Enveloppe constructible	**2 059 m²**

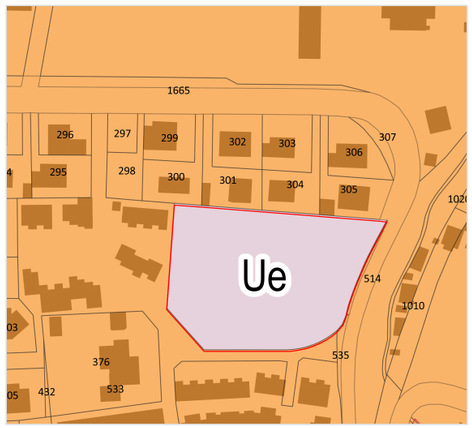

PLU 2025 — zonage Ue de BH 513 · planche n°2

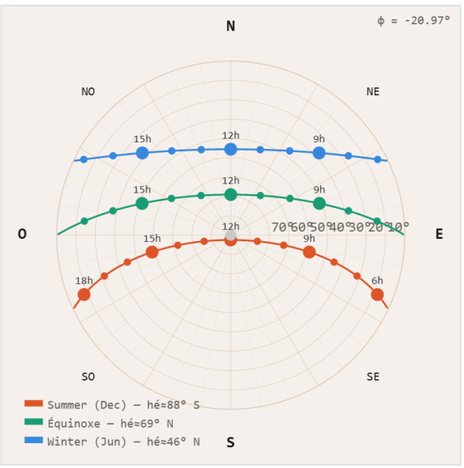

Héliodon TERLAB — ensoleillement de l'assiette



Scénario retenu — plan masse coté (BVE)

PRINCIPE

Deux lames R+3 à coursives, orientées nord-nord-est / sud-sud-ouest, tenues à distance du lot SIDR, autour d'une **cour plantée** réservée aux résidents. Le **stationnement** est regroupé en haut de parcelle, à 1,5 m des limites, desservi depuis le chemin à l'est ; les deux lames se prolongent au-dessus de ce parking (A' et B', sur poteaux) jusqu'à leurs escaliers et ascenseurs, reliés par une passerelle.

- **Bât. A** (est) : micro-crèche au RDC (entrée à l'est, jardin de 20 m²), services FJT et salle collective au sud ; logements aux étages.
- **Bât. B** (ouest) : bureaux FJT au nord et **pôle administratif MLE** au sud (accueil du public sur le chemin) ; logements aux étages.
- Entrées séparées : résidence à l'est près de l'accès véhicules, crèche à l'est, public MLE au sud-ouest ; partie clôturée MLE + services FJT au RDC.
- RDC calé au-dessus du terrain naturel (B3), sans sous-sol ; toitures 4 pans à 22°, débords 0,80 m.

CHIFFRES CLÉS

Assiette FJT (après division SIDR)	**2 965 m²**
Enveloppe constructible (reculs 3 / 4 / 4 m, hors B2u)	**2 059 m²**
Logements	**60 (50 T1 · 7 T1 bis · 3 T2)**
Surface habitable (SHAB)	**1 401 m²**
Locaux annexes (SU) : communs FJT, micro-crèche, pôle MLE	**484 m²**
Surface de plancher	**2 299 m² (cible 2 234)**
Emprise bâtie	**1 002 m² (34 %)**
Hauteur	**R+3 · faîtage 129,27 à 129,75 m NGR (≈ 13,9 m)**
Stationnement	**35 pl. pour 34 (FJT 21, Pôle MLE 7, Micro-crèche 6)**
Arbres	**11 abattus · 19 replantés**



Depuis l'accès véhicules — stationnement sous A' et B' (IA, non contractuelle)



La cour entre les lames (IA, non contractuelle)



LÉGENDE

Limites et bâti

- assiette FJT (2 965 m²)
- enveloppe constructible
- lames A et B, R+3, toiture 4 pans
- prolongements A' et B' sur poteaux
- stationnement (35 pl.)
- lot SIDR (PC NKN)
- B2u (+1 m), inconstructible
- arbre abattu (11)

Espaces extérieurs par fonction

- Cour, jardin commun
- Équipement, salle collective
- Crèche, école (cour)

Clôtures (projet BVE)

- grillage doublé d'une haie · 43 ml
- grille sur bahut doublée d'une haie · 102 ml
- portillon (5)
- portail battant, accès véhicules (1)

Accès

- accès véhicules
- entrées piétonnes : résidents, FJT, crèche, public MLE

Orthophoto IGN (Géoplateforme, 2026) · repère maquette, RGR92 UTM 40S · échelle 1/500 sur A3 (barre graphique : 20 m) · lames et prolongements sur poteaux d'après la sonde BVE · voisins SIDR d'après le PC (NKN, sept. 2026) · clôtures d'après le projet BVE · fonctions et teintes des espaces : catalogue USAGES de BVE.




Rez-de-chaussée (± 0,00 : 115,41 à 115,89 m NGR) — communs FJT, micro-crèche, pôle MLE, salle collective ; parking sous A' et B'



Étage courant, R+1 (+ 3,00) — logements en travées, coursives sur la cour

Appartement type T1s · Bât. A · R+1

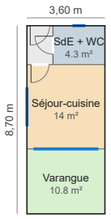


pièce	aire	minimum	dim.	état
Entrée	2,16 m²	—	1,20 / 1,2	ok
SdE + WC	4,32 m²	3,0 m²	1,80 / 1,5	ok
Séjour-cuisine	14,04 m²	14,0 m²	3,60 / 2,4	ok
Varangue	10,80 m²	—	—	—

SHAB 20,52 m² pour une cible de 20 m² (+2.6 %)
conforme aux minima

T1 (cible 20 m²)

Appartement type T1bis · Bât. B · R+3

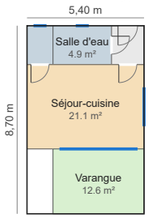


pièce	aire	minimum	dim.	état
WC	2,16 m²	—	1,20 / 0,9	ok
Salle d'eau	4,86 m²	3,0 m²	1,80 / 1,5	ok
Entrée	2,70 m²	—	1,50 / 1,2	ok
Séjour-cuisine	21,06 m²	14,0 m²	3,90 / 2,4	ok
Varangue	12,60 m²	—	—	—

SHAB 30,78 m² pour une cible de 30 m² (+2.6 %)
conforme aux minima

T1 bis

Appartement type T2 · Bât. A · R+1

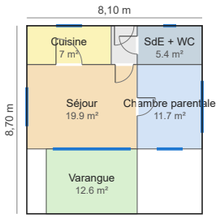


pièce	aire	minimum	dim.	état
Cuisine	7,02 m²	4,5 m²	1,80 / 1,8	ok
Entrée	2,16 m²	—	1,20 / 1,2	ok
SdE + WC	5,40 m²	3,0 m²	1,80 / 1,5	ok
Séjour	19,89 m²	14,0 m²	3,90 / 2,4	ok
Chambre parentale	11,70 m²	9,0 m²	3,00 / 2,4	ok
Varangue	12,60 m²	—	—	—

SHAB 46,17 m² pour une cible de 46 m² (+0.4 %)
conforme aux minima


T2 (cible 46 m²)

Plans de la planche BVE, recadrés sur les bâtiments (échelle ≈ 1/250) ; trame 0,30 m ; profondeur utile 5,70 m ; varangue 1,20 m sur l'extérieur pour chaque logement.


Coupe AA — transversale au droit des deux lames (regard vers le nord-nord-est) · lot SIDR à gauche (ouest), chemin Mille Roches à droite (est)

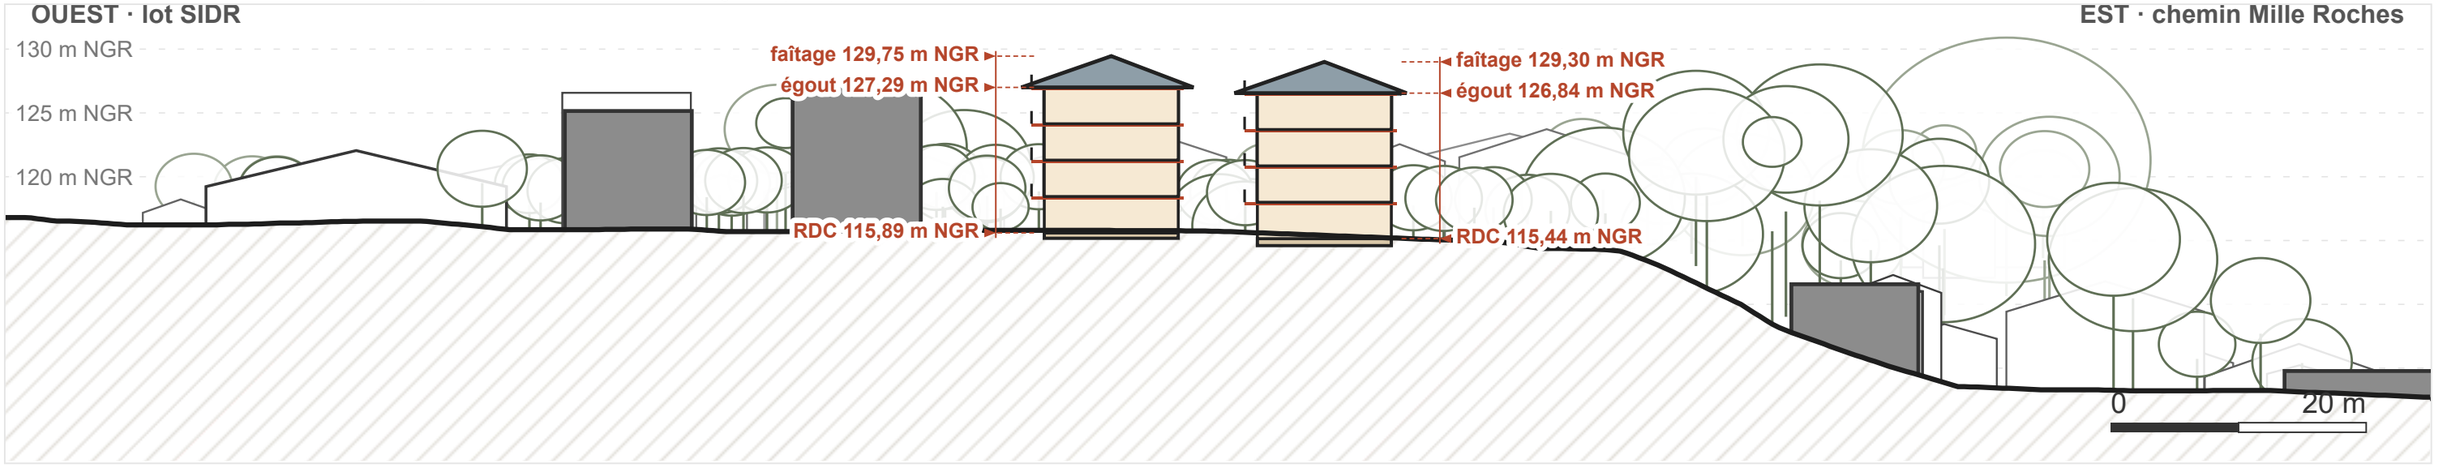

Façade urbaine est — depuis le chemin Mille Roches (regard vers l'ouest-nord-ouest) · lames A et B en premier plan, A' et B' sur poteaux au fond

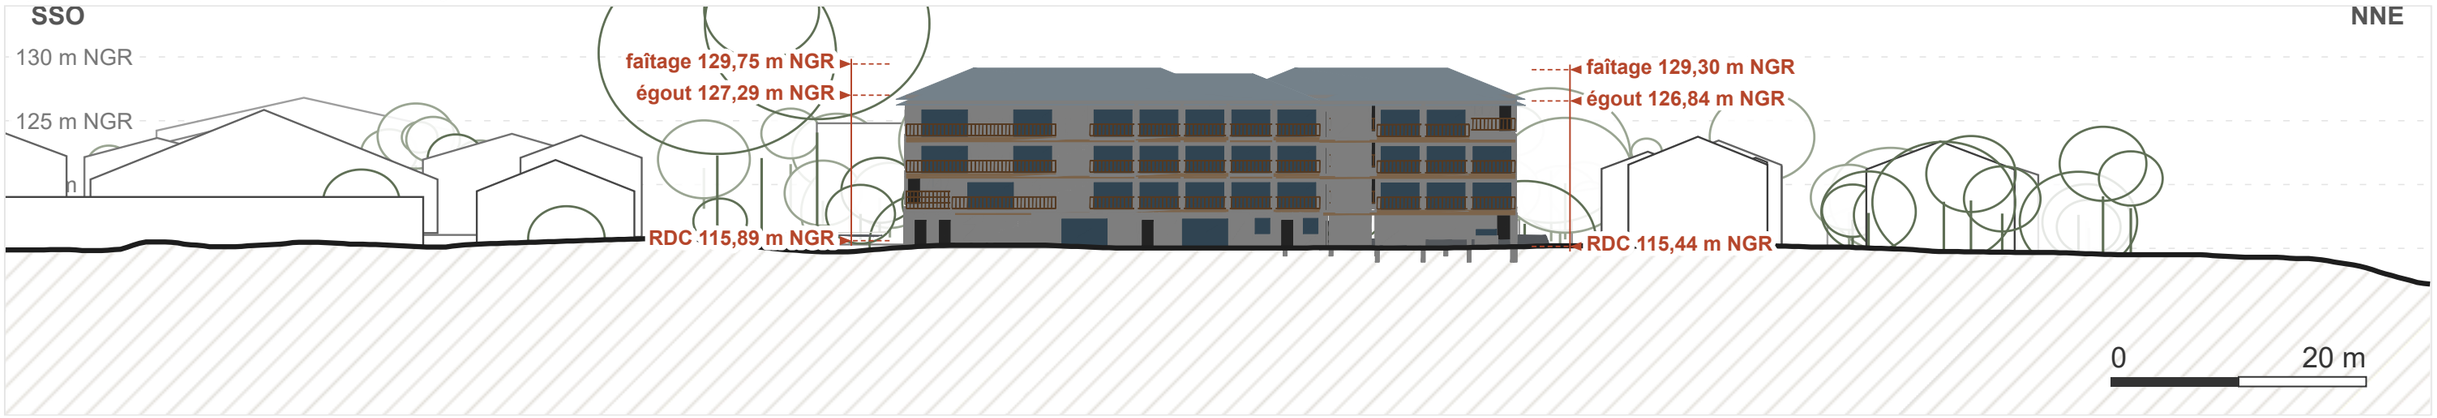


Façade urbaine sud — depuis le chemin Mille Roches (regard vers le nord)

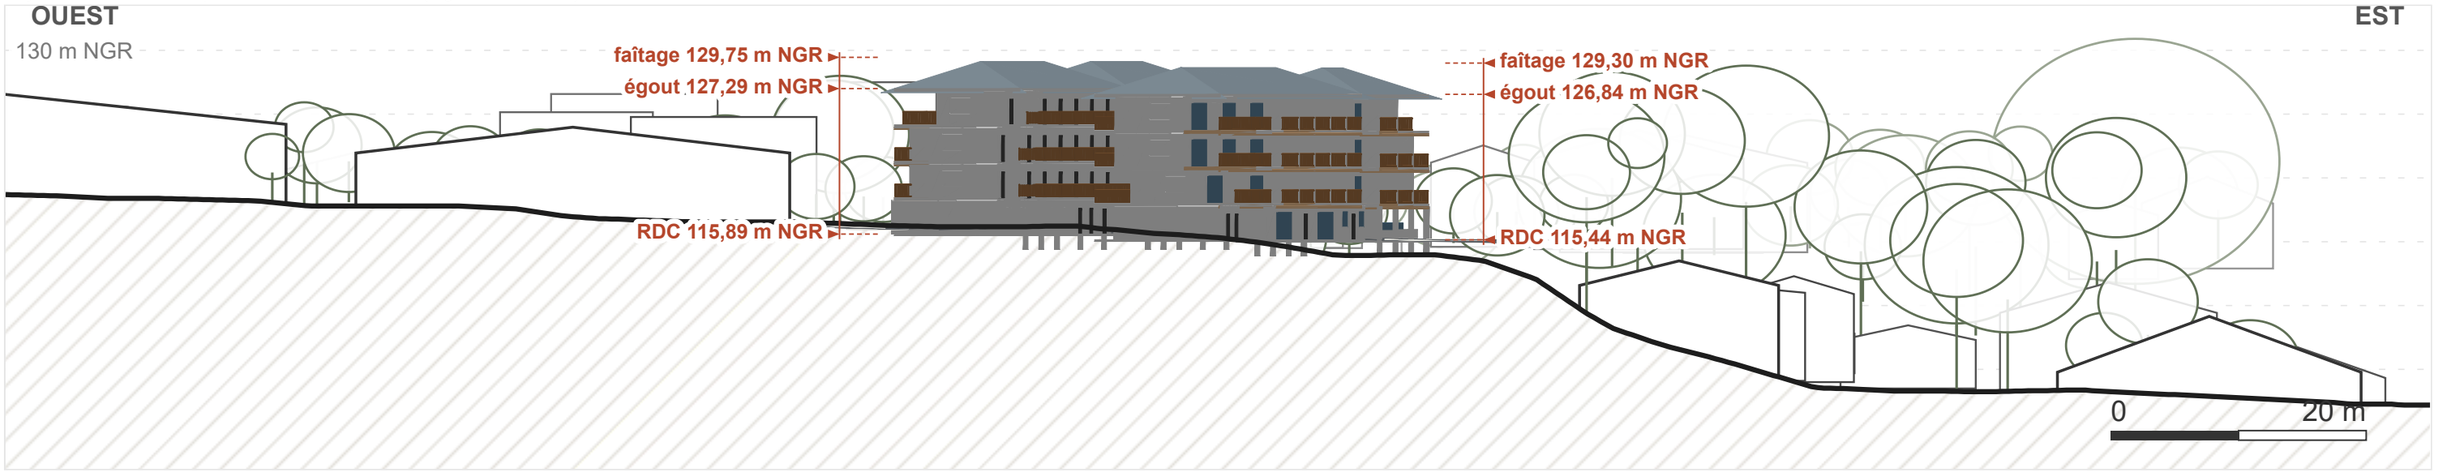

Terrain naturel : maillage de la maquette (IGN RGE ALTI / LiDAR HD), trait fort · bâti existant : IGN BD TOPO (hauteurs mesurées), voisins SIDR d'après le PC, trait gris selon la profondeur · arbres : LiDAR HD, 11 abattus ôtés · projet : RDC 115,41 à 115,89 m NGR, niveaux de 2,85 m, toitures 4 pans 22°, débord 0,80 m · cotes en m NGR · façades projetées depuis le GLB détaillé de la maquette (une teinte par matériau).

Coupe territoriale des Hauts à l'océan (≈ 10 km, axe OSO → ENE) — échelle ≈ 1/25 000, hauteurs ×3

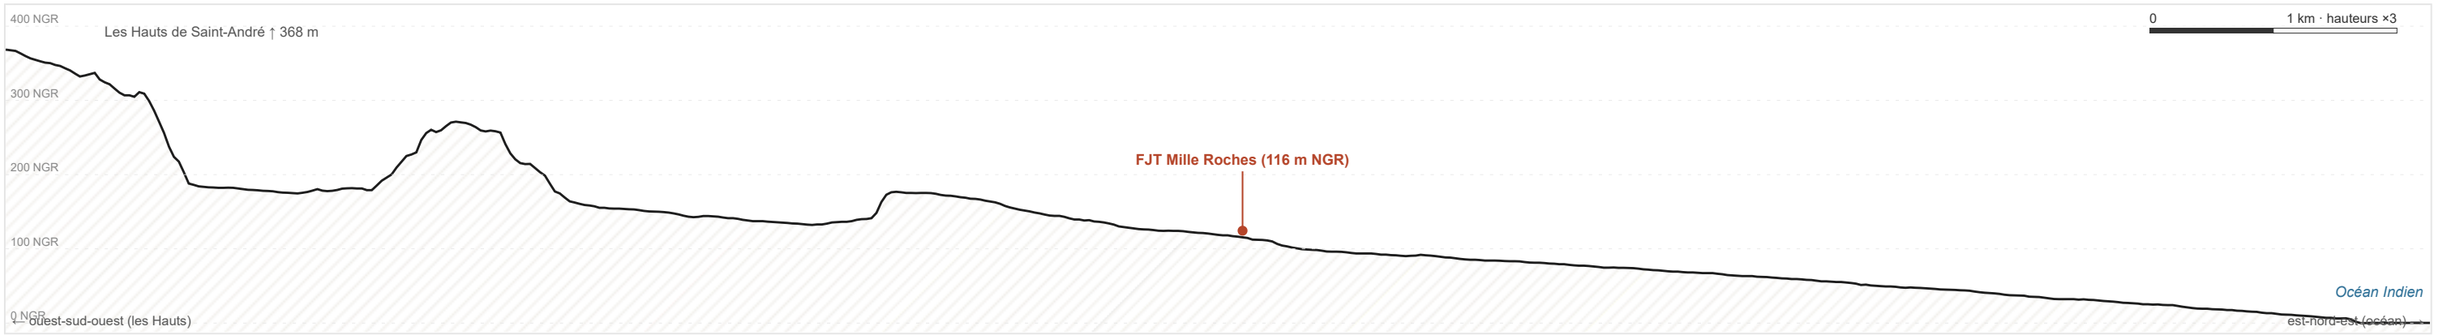

LECTURE

Mille Roches est posé à mi-pente (≈ 116 m NGR) entre les Hauts de Saint-André et le littoral, sur le rebord d'un plateau ; à l'est un talus d'une dizaine de mètres (ravine, B2u) descend vers la plaine de la Rivière du Mât.

Les deux lames R+3 (faîtage 129,27 à 129,75 m NGR) restent dans l'épannelage des collectifs voisins, dont les bâtiments SIDR R+3, et sous la ligne des grands arbres du talus.

CONSÉQUENCES POUR LE PROJET

- Conserver la **lisière arborée du talus** (B2u non bâtie) : filtre visuel et hydraulique.
- 11 arbres abattus, 19 replantés (cour, abords du parking).
- Eaux pluviales gérées à la parcelle avant le talus — pas de rejet direct dans la pente.



Vue aérienne depuis le sud-ouest — les deux lames, le stationnement en haut de parcelle, la cour plantée



Depuis le chemin Mille Roches — clôture sur voie, entrée piétonne



La cour entre les lames — coursives, passerelles, clôture ajourée de la cour

Vues de la maquette 3D BVE (IGN BD TOPO, RGE ALTI, LiDAR HD, orthophoto IGN), volumétries indicatives. Perspectives d'ambiance générées par IA (Leonardo, Nano Banana) à partir des vues de base de la maquette détaillée, contrôlées avant génération (baies, varangues, coursives, toitures 4 pans, RDC réel, clôtures) : images **non contractuelles**, matériaux et ambiance indicatifs.

PROGRAMME PAR BÂTIMENT ET PAR NIVEAU

Bât.	Niveau	Destination	T1	T1 bis	T2	SHAB m²	Annexes SU m²	SDP m²
Bât. A	RDC	Communs FJT · Extérieurs · Micro-crèche	—	—	—	—	241,0	293,9
Bât. A	R+1	Logements · Communs FJT	5	—	1	145,1	20,0	201,3
Bât. A	R+2	Logements	6	—	1	169,3	—	206,5
Bât. A	R+3	Logements	6	—	1	169,3	—	206,5
Total Bât. A			**17**	**0**	**3**	**483,7**	**261,0**	**908,2**
Bât. B	RDC	Communs FJT · Pôle admin MLE	—	—	—	—	223,0	272,0
Bât. B	R+1	Logements	7	—	—	143,6	—	175,1
Bât. B	R+2	Logements	7	—	—	143,6	—	175,1
Bât. B	R+3	Logements	5	1	—	133,4	—	162,7
Total Bât. B			**19**	**1**	**0**	**420,6**	**223,0**	**784,9**
Bât. A' (sur parking)	RDC	Rez-de-chaussée sur poteaux — stationnement	—	—	—	—	—	—
Bât. A' (sur parking)	R+1	Logements	3	—	—	64,9	—	79,1
Bât. A' (sur parking)	R+2	Logements	3	—	—	64,9	—	79,1
Bât. A' (sur parking)	R+3	Logements	2	—	—	43,3	—	52,8
Total Bât. A' (sur parking)			**8**	**0**	**0**	**173,1**	**—**	**211,0**
Bât. B' (sur parking)	RDC	Rez-de-chaussée sur poteaux — stationnement	—	—	—	—	—	—
Bât. B' (sur parking)	R+1	Logements	2	2	—	108,0	—	131,7
Bât. B' (sur parking)	R+2	Logements	2	2	—	108,0	—	131,7
Bât. B' (sur parking)	R+3	Logements	2	2	—	108,0	—	131,7
Total Bât. B' (sur parking)			**6**	**6**	**0**	**324,0**	**—**	**395,1**
TOTAL — 60 logements			**50**	**7**	**3**	**1401,4**	**484,0**	**2299,2**

SYNTHÈSE

Logements	60	50 T1 + 7 T1 bis + 3 T2
Surface habitable (SHAB)	1401,4 m²	moyenne 23,4 m² / logement
Locaux annexes (SU)	484,0 m²	communs FJT, micro-crèche 100 m², pôle MLE 151 m²
Surface de plancher	2299,2 m²	cible 2 234 m² (+3 %)
Ratio SHAB / SDP	0,61	coursives extérieures hors SDP
Emprise bâtie	1 002 m²	34 % de l'assiette (CES maximal 0.6)
Stationnement	35 pl.	besoin 34 (FJT 21, Pôle MLE 7, Micro-crèche 6) · haut de parcelle 23 · allée 3 · chemin 3 · autres 6
Arbres	11 / 19	abattus / replantés
Clôture — grillage doublé d'une haie	43 ml	4 tronçon(s)
Clôture — grille sur bahut doublée d'une haie	102 ml	1 tronçon(s)
Ouvertures	6	5 portillon · 1 battant

Type	Nombre	Surface cible	SHAB cible cumulée
T1	50	20 m²	1 000 m²
T1 bis	7	30 m²	210 m²
T2	3	46 m²	138 m²

SHAB : surface habitable ; SU annexes : communs FJT, micro-crèche, pôle MLE ; SDP : pré-dimensionnement ±10 % (coursives hors SDP). Source : sonde BVE « opération collective », projet MGA-26-04.

POINTS DE VIGILANCE

1. **PLU 2025 — zone Ue** : l'hébergement (FJT) y est **interdit**. Évolution du PLU à engager avec la Ville, en commun avec l'opération SIDR.
2. **Assiette** : plan de division et servitude de réseaux à obtenir (SEMAC, NKN, géomètre).
3. **PPRN** : cote de référence B3 à obtenir ; l'accès véhicules traverse la bande B2u : à faire valider.
4. **Stationnement** : 35 places pour un besoin estimé de 34 (MLE et crèche à confirmer avec l'exploitant).
5. **Programme** : salle collective de 75 m² à confirmer ; place du pôle MLE et de la micro-crèche validée sur le principe.
6. **Topographie** : relevé géomètre à commander ; l'étude repose sur le LiDAR HD IGN (≈ 10 cm).
7. **Alertes de la sonde BVE** : réserve de stationnement sur une servitude (73.47 m²) : admis, à confirmer.

SUITE PROPOSÉE

- Réunion Ville / SEMAC / SIDR sur l'évolution du PLU.
- Plans types T1, T1 bis et T2 calés sur le programme.
- Estimation des travaux et montage (LLTS, FSE, bonus EPFR).
- Perspectives d'ambiance contrôlées pour la présentation aux élus.