

Image d'ambiance générée par IA à partir de la maquette 3D — non contractuelle

semac
SOCIÉTÉ D'ÉCONOMIE MIXTE
D'AMÉNAGEMENT ET DE CONSTRUCTION

Etude de faisabilité · capacité

Foyer de Jeunes Travailleurs

Mille Roches, Saint-André


ind 0 — document de travail
SEPTEMBRE 2026

Adresse	573 chemin Mille Roches, 97440 Saint-André
Cadastre	BH 513 pour partie (4 951 m²)
Assiette FJT	≈ 2 960 m² — hypothèse de découpage, à valider
Programme	FJT 60 logements LLTS · exploitant MLE
Zone PLU	**Ue** — équipements (PLU approuvé le 02/07/2025) · hébergement interdit : évolution du PLU requise
PPRN	B3 inondation (≈ 95 %) · B2u en limite est

Mathias Giraud Architecture mgA.




Situation — orthophoto IGN · parcelle BH 513, lot SIDR (bleu), assiette FJT (jaune)

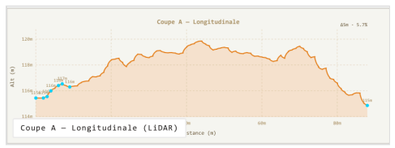

Profil longitudinal LiDAR (Δ 5 m · 5,7 %)



Profil transversal LiDAR (Δ 2 m · 2,7 %)

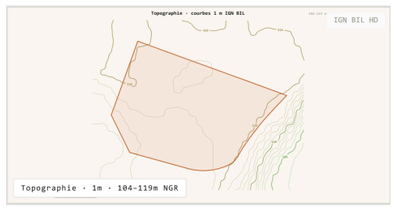

Courbes 1 m — IGN RGE ALTI

LE SITE

Friche arborée de 4 951 m² au cœur du quartier Mille Roches (NPNRU), bordée au sud, à l'ouest et à l'est par le chemin Mille Roches (chaussée 4 m), au nord par un tissu de cases et de petits collectifs. Plateau quasi plan entre **114,8 et 117,7 m NGR** ; la limite est surplombe une ravine (talus, courbes serrées). Climat de la côte au vent : **alizés d'est**, pluviométrie ≈ **2 365 mm/an**.

RISQUES — PPRN SAINT-ANDRÉ (BRGM 2026)

- **B3 — inondation, prescriptions** : ≈ 4 716 m² de la parcelle. Constructible sous réserve de caler les planchers au-dessus de la cote de référence ; **pas de sous-sol** ; clôtures transparentes hydrauliquement.
- **B2u — inondation + mouvement de terrain** : couloir de la ravine à l'est, ≈ 246 m² sur la parcelle dont ≈ 100 m² sur le lot FJT, laissés libres de construction.
- Zone rouge **R1** (interdiction) au sud-est, hors parcelle.
- Servitude PM1 (PPR) reportée au GPU.

PLU APPROUVÉ LE 02/07/2025 — ZONE UE

BH 513 est intégralement classée en **zone Ue** (« zones d'équipements » : stades, gymnases, services techniques…), au sein de la zone Ub. Aucune OAP, aucun emplacement réservé ni EBC sur la parcelle (planche n°2 Centre-ville / Cressonnière).

> **Point bloquant** — en Ue, la sous-destination **« hébergement » est interdite** et le logement n'est admis que pour le gardiennage (70 m² de SDP). Un FJT relève de l'hébergement (« foyers de travailleurs », art. R151-28). Le projet — comme les 20 LLS de la SIDR — suppose une **évolution du PLU** (modification ou déclaration de projet emportant mise en compatibilité, reclassement en Ub), ou une qualification en équipement d'intérêt collectif à faire valider par le service instructeur.


Règles Ue retenues pour l'étude : hauteur **16 m** (R+3 ≈ 12,6 m à l'égout : conforme) ; recul **3 m** sur voie ; **4 m** sur limites séparatives et de fond ; pas de ratio de stationnement imposé (le programme retient 1 place / 3 lgts) ; **pas de blanc en paroi** ni de tôle non peinte ; sol protégé du soleil sur 3 m au droit de 50 % des façades.

PROGRAMME (CR VILLE / MLE / SEMAC DU 26/06/2026)

- P1 — FJT : **60 logements** — 50 T1 de 20 m² et 10 T2 d'≈ 46 m², produit LLTS
- Deux bâtiments privilégiés, **R+3 maximum**
- Stationnement en surface : **1 place pour 3 logements**
- Bureaux MLE et crèche : hors de cette assiette (programme recentré sur le FJT)



Hypothèse de découpage BH 513 — lot SIDR au nord (≈ 2 000 m²), assiette FJT au sud (≈ 2 960 m²), enveloppe constructible (tirets orange), B2u (hachures rouges), servitude réseaux (tirets bleus)

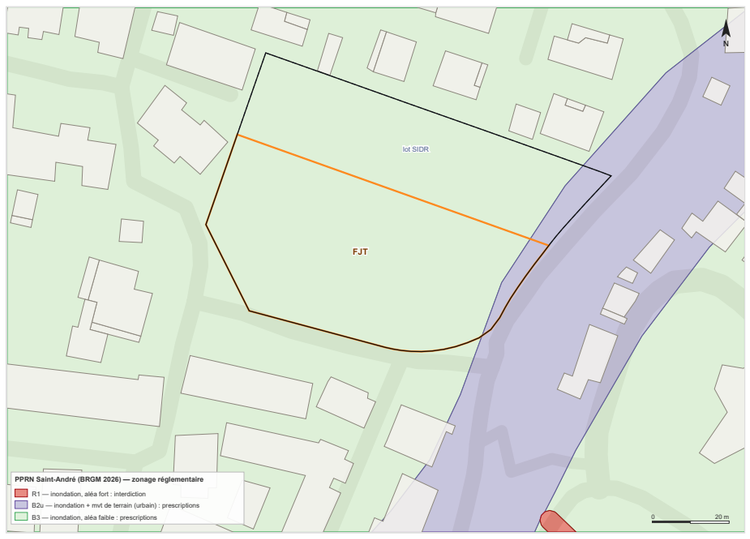

PPRN approuvé (BRGM 2026, PEIGEO) — lot FJT : B3 ≈ 2 870 m², B2u ≈ 100 m² ; R1 hors parcelle (sud-est)

LECTURE DU COURRIEL SEMAC DU 16/09

- ≈ 2 000 m² cédés à la SIDR pour 20 LLS (programmation 2027, PC fin 09/2026, MOE NKN) — la partie déjà levée par le géomètre.
- ≈ 3 000 m² pour le FJT (programmation 2028) — la partie **sans relevé topographique**.
- La SEMAC doit une **servitude de réseaux** au lot SIDR : le lot SIDR n'a donc pas d'exutoire direct vers le point bas.


HYPOTHÈSE RETENUE

Le lot SIDR occupe la bande nord, parallèle à la limite nord-est (profondeur ≈ 22 m), au contact des cases existantes ; le FJT occupe la partie sud, avec façade sur le chemin Mille Roches sur trois côtés. La servitude (4 m) longe la limite ouest du lot FJT vers le point bas sud-ouest, sous le parking.

> **À valider avant toute suite** avec la SEMAC et la MOE SIDR (E. Naiken, NKN) sur la base du plan topographique et de division *2026-004-409BH513-SIDR-Client.dwg* : tracé exact de la limite, position de la servitude, accès.

ENVELOPPE CONSTRUCTIBLE FJT

Assiette FJT	**2 962 m²**
Reculs Ue : voie 3 m · limites 4 m	—
Hors B2u (+1 m) et servitude	—
Enveloppe constructible	**2 242 m²**

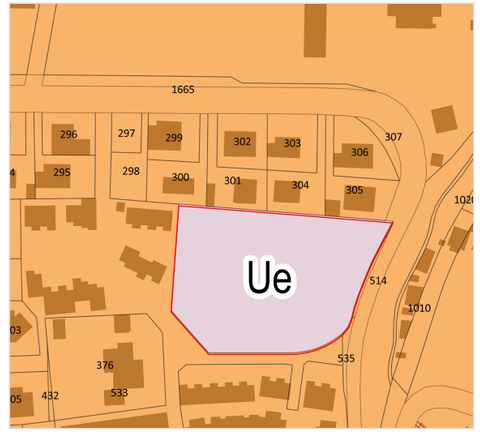


PLU 2025 — zonage Ue de BH 513 (contour cadastral en rouge) · planche n°2

Même programme (60 logements, R+3), même enveloppe Ue (2 242 m²) et même parking : cinq familles d'implantation testées géométriquement, puis quatre modes de distribution du T1. La profondeur constructible (≈ 36 m entre la limite SIDR et le chemin) ne laisse passer que des **lames** ; les plots sont écartés.

O1 · Deux lames parallèles, jardin central


retenu

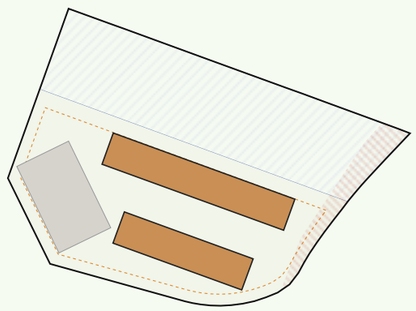

Bâtiments	**2**
Emprise	**738 m² (25 %)**
Prospect mini	**9.7 m**
Espaces libres	**≈ 50 %**

- Coursives sur jardin, logements mono-orientés + varangue
- Ventilation traversante par imposte sur coursive
- Jardin central ≈ 10 m (noue GIEP)


O2 · Lames décalées en redents

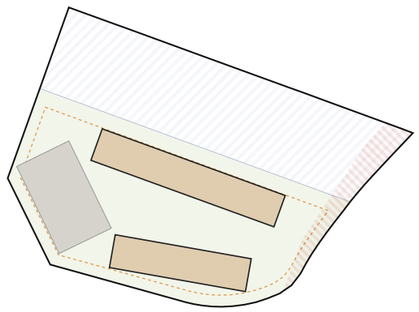

Bâtiments	**2**
Emprise	**738 m² (25 %)**
Prospect mini	**9.7 m**
Espaces libres	**≈ 50 %**

- Coursives sur jardin, logements mono-orientés + varangue
- Ventilation traversante par imposte sur coursive
- Jardin central ≈ 10 m (noue GIEP)


O3 · Bâtiment en T (un seul volume)

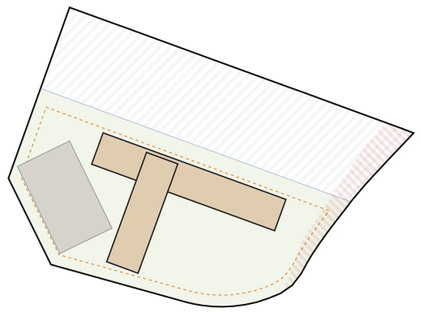

Bâtiments	**1**
Emprise	**690 m² (23 %)**
Prospect mini	**—**
Espaces libres	**≈ 52 %**

- Un seul bâtiment : 1 noyau, gestion simplifiée
- Angles intérieurs : logements peu ventilés, vis-à-vis
- Jardin coupé en deux cours


O4 · Lame unique à couloir central

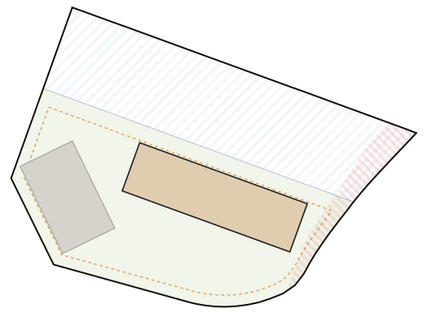

Bâtiments	**1**
Emprise	**607 m² (20 %)**
Prospect mini	**—**
Espaces libres	**≈ 55 %**

- Compacité maximale, un seul noyau, emprise mini
- Logements mono-orientés sans ventilation traversante (RTAA DOM)
- Couloir intérieur à éclairer / ventiler : à éviter en climat tropical

O5 · Plots (2 à 3 plots 15 × 15 m)

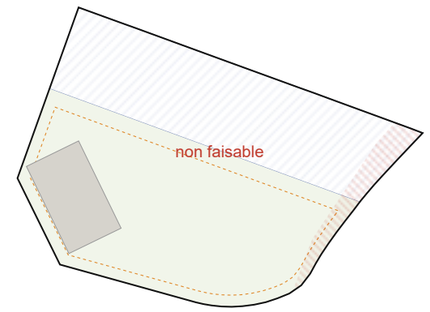

Non faisable dans l'enveloppe

- Testé : profondeur constructible ≈ 36 m < lame 8,6 + 8 m + plot 15 m
- Aucune combinaison de plots à 8 m de prospect avec le parking
- Écarté (supposerait R+4 ou parking réduit)

DISTRIBUTION DES LOGEMENTS — T1 DE 20 M²

T1 sur coursive + varangue intégrée

retenu




- 20 m² + varangue 2,3 m²
- ventilation traversante (imposte sur coursive)
- coursive = lieu de rencontre, contrôle social

T1 sur couloir central




- lame épaisse 13,2 m, très compacte
- mono-orienté, pas de ventilation traversante
- couloir intérieur à climatiser/éclairer

T1 d'angle en plot

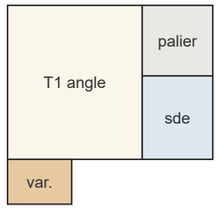


- bi-orienté, varangue d'angle
- 4 à 6 lgts par palier
- noyaux plus nombreux (coût, gestion)

T1' traversant sur palier

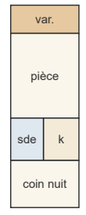

- 2 lgts / palier : pas de coursive
- traversant idéal, mais noyaux ×3
- surface ≈ 25 m² (hors cible 20 m²)

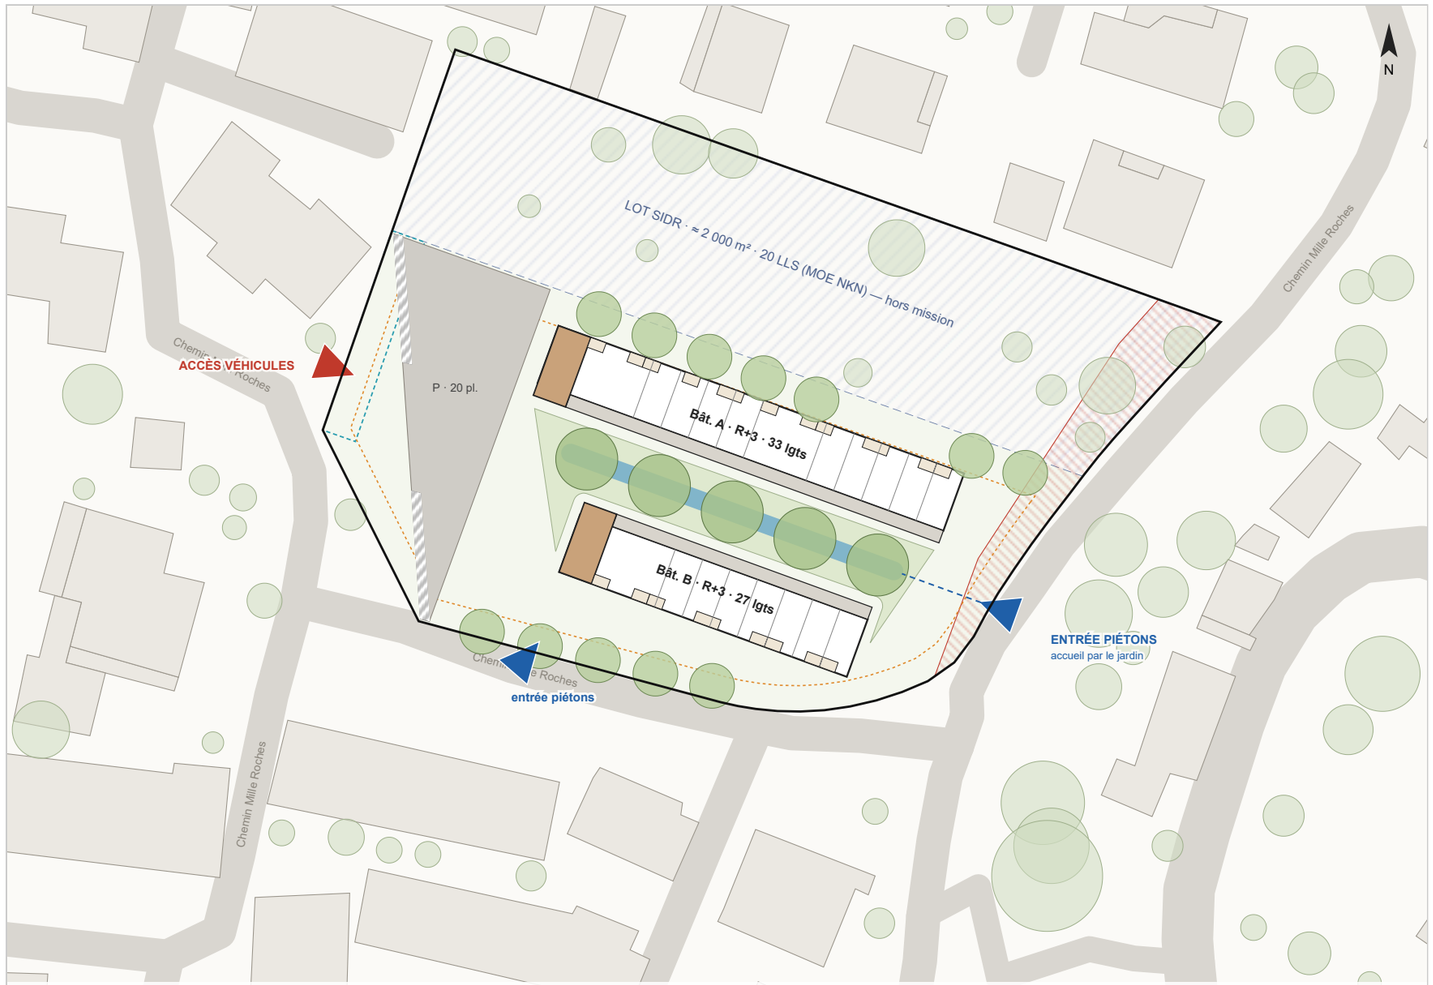

Variante 1 — deux lames parallèles, jardin central — plan masse

PRINCIPE

Deux lames R+3 parallèles à l'axe de la parcelle (orientation NNE / SSO), à coursives **tournées vers un jardin central** de ≈ 10 m de large qui porte la noue GIEP. Le bâtiment A (au nord, 50 m) accueille au RDC les espaces communs du foyer — accueil, bureau du gestionnaire, permanence MLE, salle collective, laverie — et tient la limite avec le lot SIDR ; le bâtiment B (au sud, 36 m) tient le chemin Mille Roches. Le parking, à l'ouest sur la servitude, est tracé aux normes (bataille, allée 5,50 m, NF P 91-100) : 27 places dont 1 PMR pour 20 requises, la réserve pouvant devenir jardin ou places visiteurs.


- Logements mono-orientés côté extérieur, portes et impostes hautes sur coursive : **ventilation traversante** par les alizés d'est.
- **Varangues intégrées** jumelées deux à deux entre des trumeaux en **bardage bois** à lames verticales : écriture rythmée A-B-B-A, baies verticales ≈ 1,05 × 1,55 m (composition houseg-speech).
- Façades principales nord / sud, faciles à protéger ; enduit teinte sable (PLU : pas de blanc en paroi), toitures monopentes en tôle peinte grise, égout vers le jardin.
- RDC surélevé de ≈ 0,60 m (cote de référence B3), sans sous-sol.

CHIFFRES CLÉS

Assiette FJT (hypothèse)	**2962 m²**
Enveloppe constructible	**2 242 m²**
Logements	**60 (50 T1 · 10 T2)**
Surface habitable	**1460 m²**
Surface de plancher (≈)	**1930 m²**
Emprise bâtie	**738 m² (25 %)**
Hauteur	**R+3 · ≈ 12,6 m à l'égout**
Écart entre lames	**9.7 m**
Stationnement	**27 pl. dont 1 PMR (besoin 20)**
Espaces libres / perméables	**≈ 50 %**





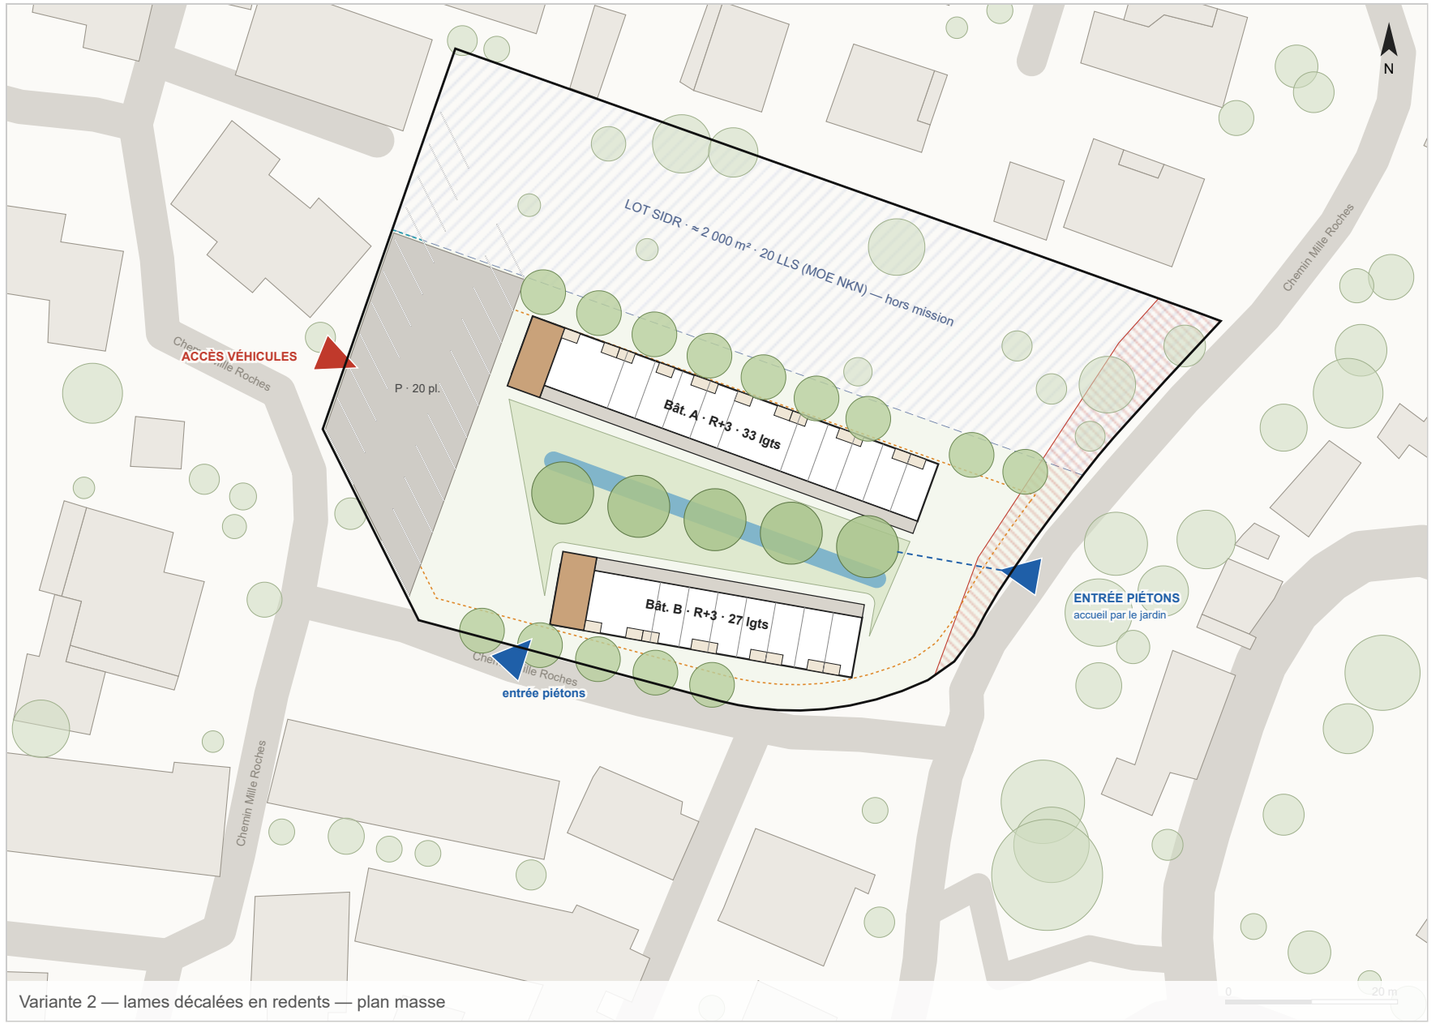

Variante 2 — lames décalées en redents — plan masse

PRINCIPE

Même programme ; le bâtiment B pivote pour **suivre le chemin Mille Roches** (≈ 5°) et se décale vers l'est : le jardin s'ouvre en biais vers la ravine et les vues lointaines, et le bâtiment A se rapproche de l'ouest. L'écart minimal entre lames passe à ≈ 9 m.

- Front bâti plus continu sur la rue, meilleure lecture de l'adresse du foyer.
- Jardin en entonnoir, plus généreux côté est, où le talus est préservé.
- Parking à l'ouest réduit à 19 places (1 de moins que le besoin) : à compenser par une place sur le chemin ou en réduisant le décalage.

CHIFFRES CLÉS

Assiette FJT (hypothèse)	**2962 m²**
Enveloppe constructible	**2 242 m²**
Logements	**60 (50 T1 · 10 T2)**
Surface habitable	**1460 m²**
Surface de plancher (≈)	**1930 m²**
Emprise bâtie	**738 m² (25 %)**
Hauteur	**R+3 · ≈ 12,6 m à l'égout**
Écart entre lames	**9.7 m**
Stationnement	**19 pl. dont 1 PMR (besoin 20)**
Espaces libres / perméables	**≈ 50 %**








Mathias Giraud Architecture mgA.	semac Société d'Économie Mixte d'Aménagement et de Construction	ÉTUDE DE FAISABILITÉ **FJT · BH 513 · Saint-André**	**Plan masse coloré — variante 1 · 1/500**	**A.6** 24/09/2026


Coupe AA — transversale nord-sud au droit des deux lames, regard vers l'ouest · 1/500 · *sud (chemin Mille Roches) à gauche, nord (lot SIDR) à droite*

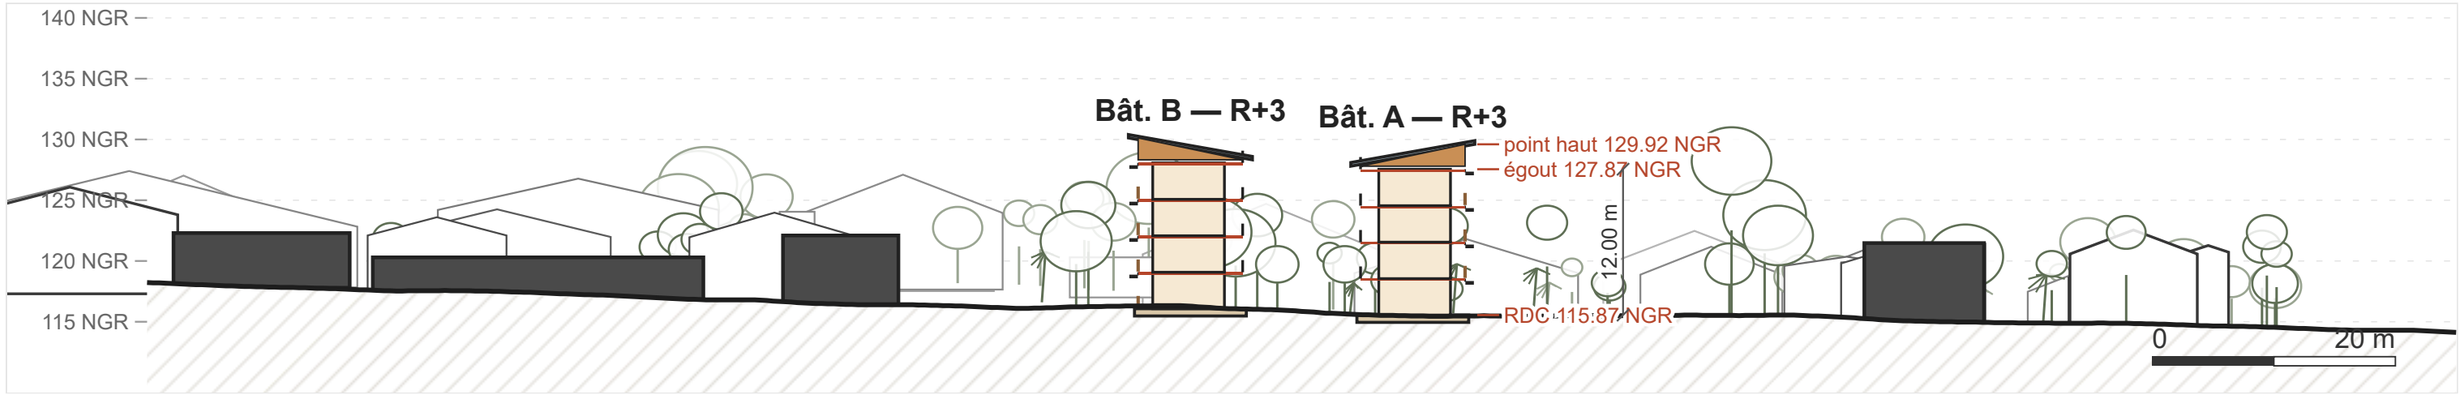

Façade urbaine sud — depuis le chemin Mille Roches, regard vers le nord · 1/500 · bâtiment B au premier plan, bâtiment A en arrière-plan




Façade urbaine ouest — depuis le chemin Mille Roches (côté parking), regard vers l'est · 1/500 · pignons bardés, monopentes

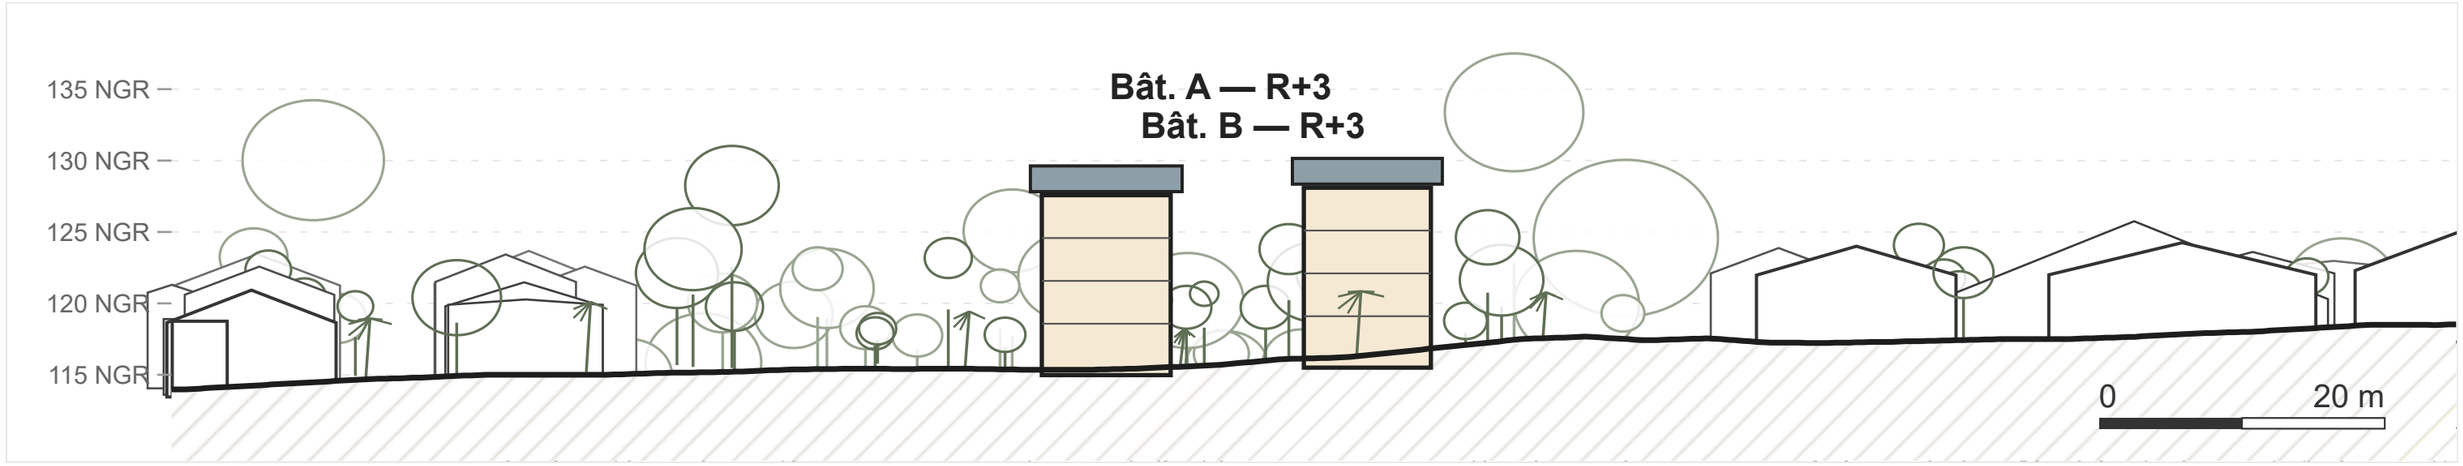


Légende — terrain naturel (IGN RGE ALTI / LiDAR HD) en trait fort, sol hachuré · bâti existant (IGN BD TOPO, hauteurs mesurées) en gris, dégradé selon la profondeur ; sa partie sous le terrain naturel est masquée · arbres (LiDAR HD + semis de la maquette) au trait, ceux devant le projet en simple contour · **projet en couleur** : coupe des planchers en brique, logements en sable, varangues, bardage bois, vitrages bleus · RDC calé 0,60 m au-dessus du TN (PPR B3), niveaux de 3,00 m, varangue 1,20 m, coursive 1,50 m, toiture monopente 10° · cotes en m NGR (IGN69 / NGR Réunion).

Mathias Giraud Architecture mgA.	semac SOCIÉTÉ D'ÉCONOMIE MIXTE D'AMÉNAGEMENT ET DE CONSTRUCTION	ÉTUDE DE FAISABILITÉ **FJT · BH 513 · Saint-André**	**Coupes et façades urbaines — variante 1**	**A.7** 24/09/2026

Coupe territoriale des Hauts à l'océan (≈ 10 km, axe OSO → ENE) — échelle ≈ 1/25 000, hauteurs ×3

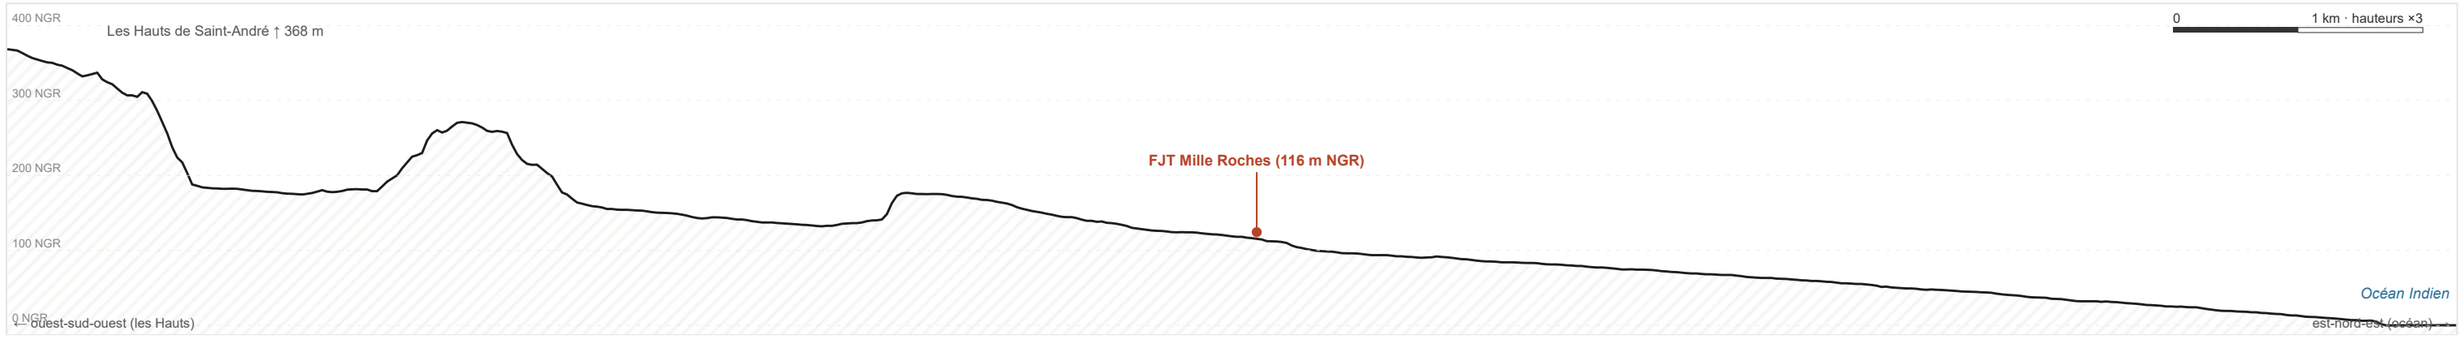

Coupe paysagère ouest → est au droit du site, 1,2 km — échelle horizontale ≈ 1/2000, hauteurs ×2

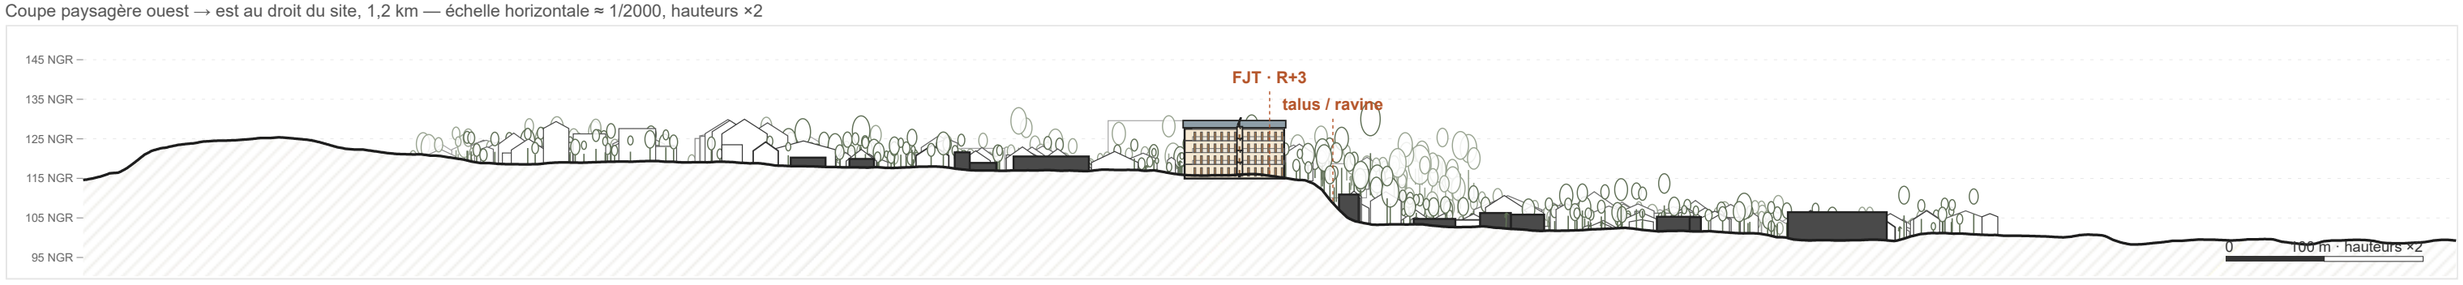

LECTURE

À l'échelle du territoire, Mille Roches est posé à mi-pente (116 m NGR) entre les Hauts de Saint-André (≈ 370 m à 5 km) et le littoral à 4,5 km, sur le glacis qui descend vers la côte au vent. Le site occupe le rebord d'un **plateau à ≈ 115-118 m NGR**, tenu à l'ouest par le tissu de cases et de collectifs du quartier Mille Roches. À l'est, un **talus d'une dizaine de mètres** (ravine, bande B2u) descend vers la plaine basse de la Rivière du Mât et de la côte.

Les deux lames R+3 (≈ 13,5 m au faîtage) restent dans l'épannelage des collectifs voisins et **ne dépassent pas la ligne des grands arbres** du talus : depuis la plaine, le projet se lit derrière le couvert végétal conservé en limite est.

CONSÉQUENCES POUR LE PROJET

- Conserver et renforcer la **lisière arborée du talus** (bande B2u non bâtie) : filtre visuel et hydraulique.
- Orienter l'**entrée piétonne et le jardin** vers l'est : vues lointaines au-dessus de la plaine.
- Gestion des eaux pluviales à la parcelle avant le talus (noue, infiltration) — pas de rejet direct dans la pente.



Vue aérienne depuis le sud-ouest — parking, lames R+3 à monopente, jardin central



Depuis le chemin Mille Roches — bâtiment B, locaux associés vitrés en RDC



Le jardin central entre les lames — coursives, noue paysagère

Images d'ambiance générées par IA (Leonardo / nano-banana) à partir des vues de la maquette 3D (IGN BD TOPO V3, RGE ALTI, LiDAR HD, orthophoto) — volumétrie calée sur la maquette, matériaux et ambiance non contractuels.

PROGRAMME PAR NIVEAU (VARIANTES 1 ET 2)

Bât.	Niveau	Destination	T1 20 m²	T2 46 m²	SHAB m²
Bât. A	RDC	Accueil, bureau gestionnaire, permanence MLE, salle collective + cuisine partagée, laverie, local vélos	—	—	—
Bât. A	R+1	Logements	9	2	272
Bât. A	R+2	Logements	9	2	272
Bât. A	R+3	Logements	9	2	272
Bât. B	RDC	3 logements PMR · **locaux associés** ouverts sur le chemin (salle d'activités / accueil associatif, atelier, local vélos) · local poubelles, local technique	2	1	86
Bât. B	R+1	Logements	7	1	186
Bât. B	R+2	Logements	7	1	186
Bât. B	R+3	Logements	7	1	186
Total			**50**	**10**	**1460**

SYNTHÈSE

Logements	60	50 T1 + 10 T2
Surface habitable (SHAB)	1460 m²	moyenne 24.3 m² / logement
Espaces communs (SU)	≈ 333 m²	RDC A + atelier RDC B
Surface de plancher	≈ 1930 m²	pré-dimensionnement ±10 %
Ratio SHAB / SDP	0.76	coursives extérieures hors SDP
Emprise bâtie	738 m²	25 % de l'assiette
Stationnement	27 pl.	dont 1 PMR (besoin programme 20 pl. = 1 / 3 lgts) · + 60 places vélos
Locaux associés RDC	≈ 90 m²	bât. B, vitrine sur le chemin Mille Roches
Espaces libres	≈ 54 %	jardin central + noue GIEP + haies

Trames : T1 3,40 × 5,90 m + varangue intégrée 1,90 × 1,20 m (≈ 2,3 m²) ; T2 7,80 × 5,90 m + varangue 3,00 × 1,20 m ; noyau escalier + ascenseur 4,00 m ; lame 8,60 m (logement 5,90 + varangue 1,20 + coursive 1,50).

POINTS DE VIGILANCE

1. **Assiette foncière** : découpage SIDR / FJT et servitude réseaux à arrêter avec la SEMAC et NKN (plan de division DWG du 17/09).
2. **PLU 2025 — zone Ue** : l'hébergement (FJT) y est **interdit**. Évolution du PLU à engager avec la Ville (reclassement en Ub par modification ou déclaration de projet), en commun avec l'opération SIDR. Hauteur (16 m) et reculs (3 / 4 m) compatibles.
3. **PPRN B3** : cote de référence à obtenir (DEAL / BRGM) — calage des RDC, transparence des clôtures, pas de sous-sol. Bande B2u inconstructible en pratique.
4. **Topographie** : relevé géomètre de l'assiette FJT à commander ; l'étude repose sur le LiDAR HD IGN (précision ≈ 10 cm).
5. **Programme d'exploitation** : surfaces des communs, bureau MLE, veille de nuit — à caler avec la MLE (via E. Hamel).
6. **GIEP** : 2 365 mm/an, zone inondable — gestion à la parcelle (noue centrale, stationnement perméable), éligible au bonus GIEP.

SUITE PROPOSÉE

- Réunion Ville / SEMAC / SIDR sur la **procédure d'évolution du PLU** (zone Ue).
- Réunion de calage SEMAC / MLE / NKN sur l'assiette et le programme.
- Choix d'une variante, plans types T1 / T2 et RDC communs.
- Estimation des travaux et montage (LLTS, FSE, bonus EPFR) — à produire sur la variante retenue.
- Perspectives d'ambiance pour la présentation aux élus.